Comune di Firenze - Piano Operativo

disciplina del suolo e degli insediamenti - scala 1:5.000 - estratto

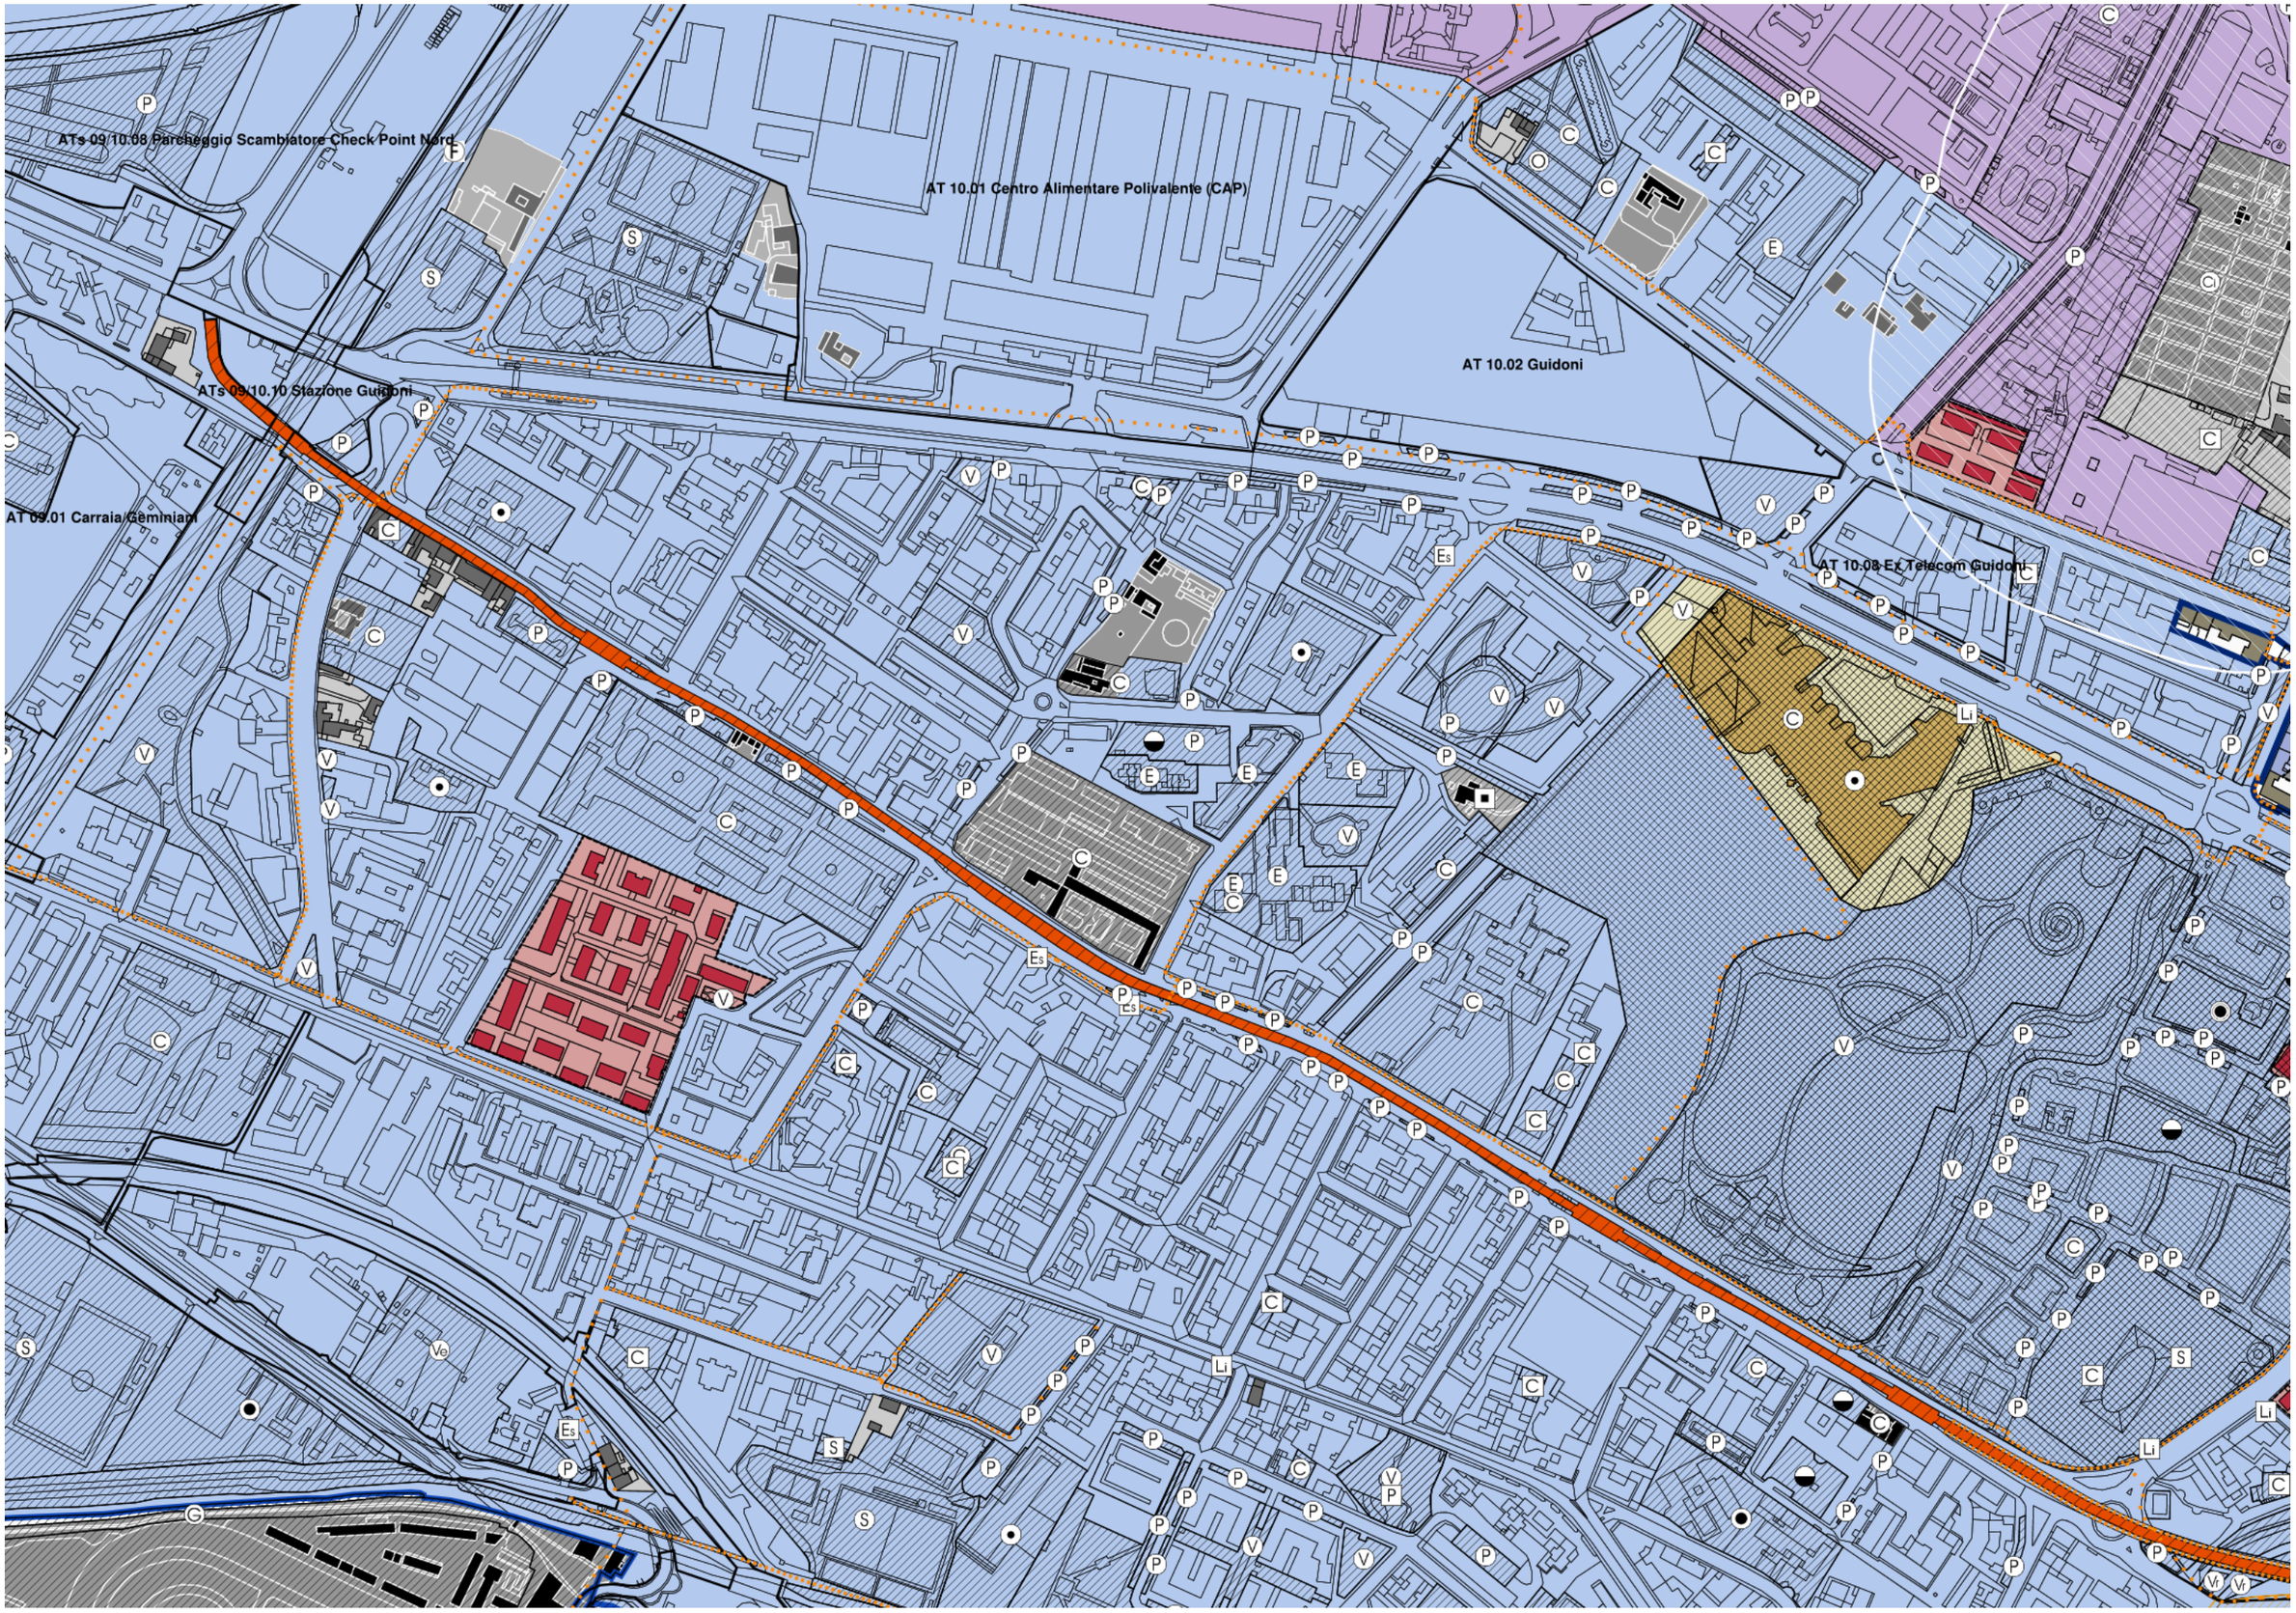

estratto alla data 20 luglio 2025

stampato il 20 luglio 2025

11 | attrezzature e spazi collettivi - scala 1:10.000 - estratto

Comune di Firenze - Piano Strutturale

9 | dotazioni ecologico ambientali - scala 1:10.000 - estratto

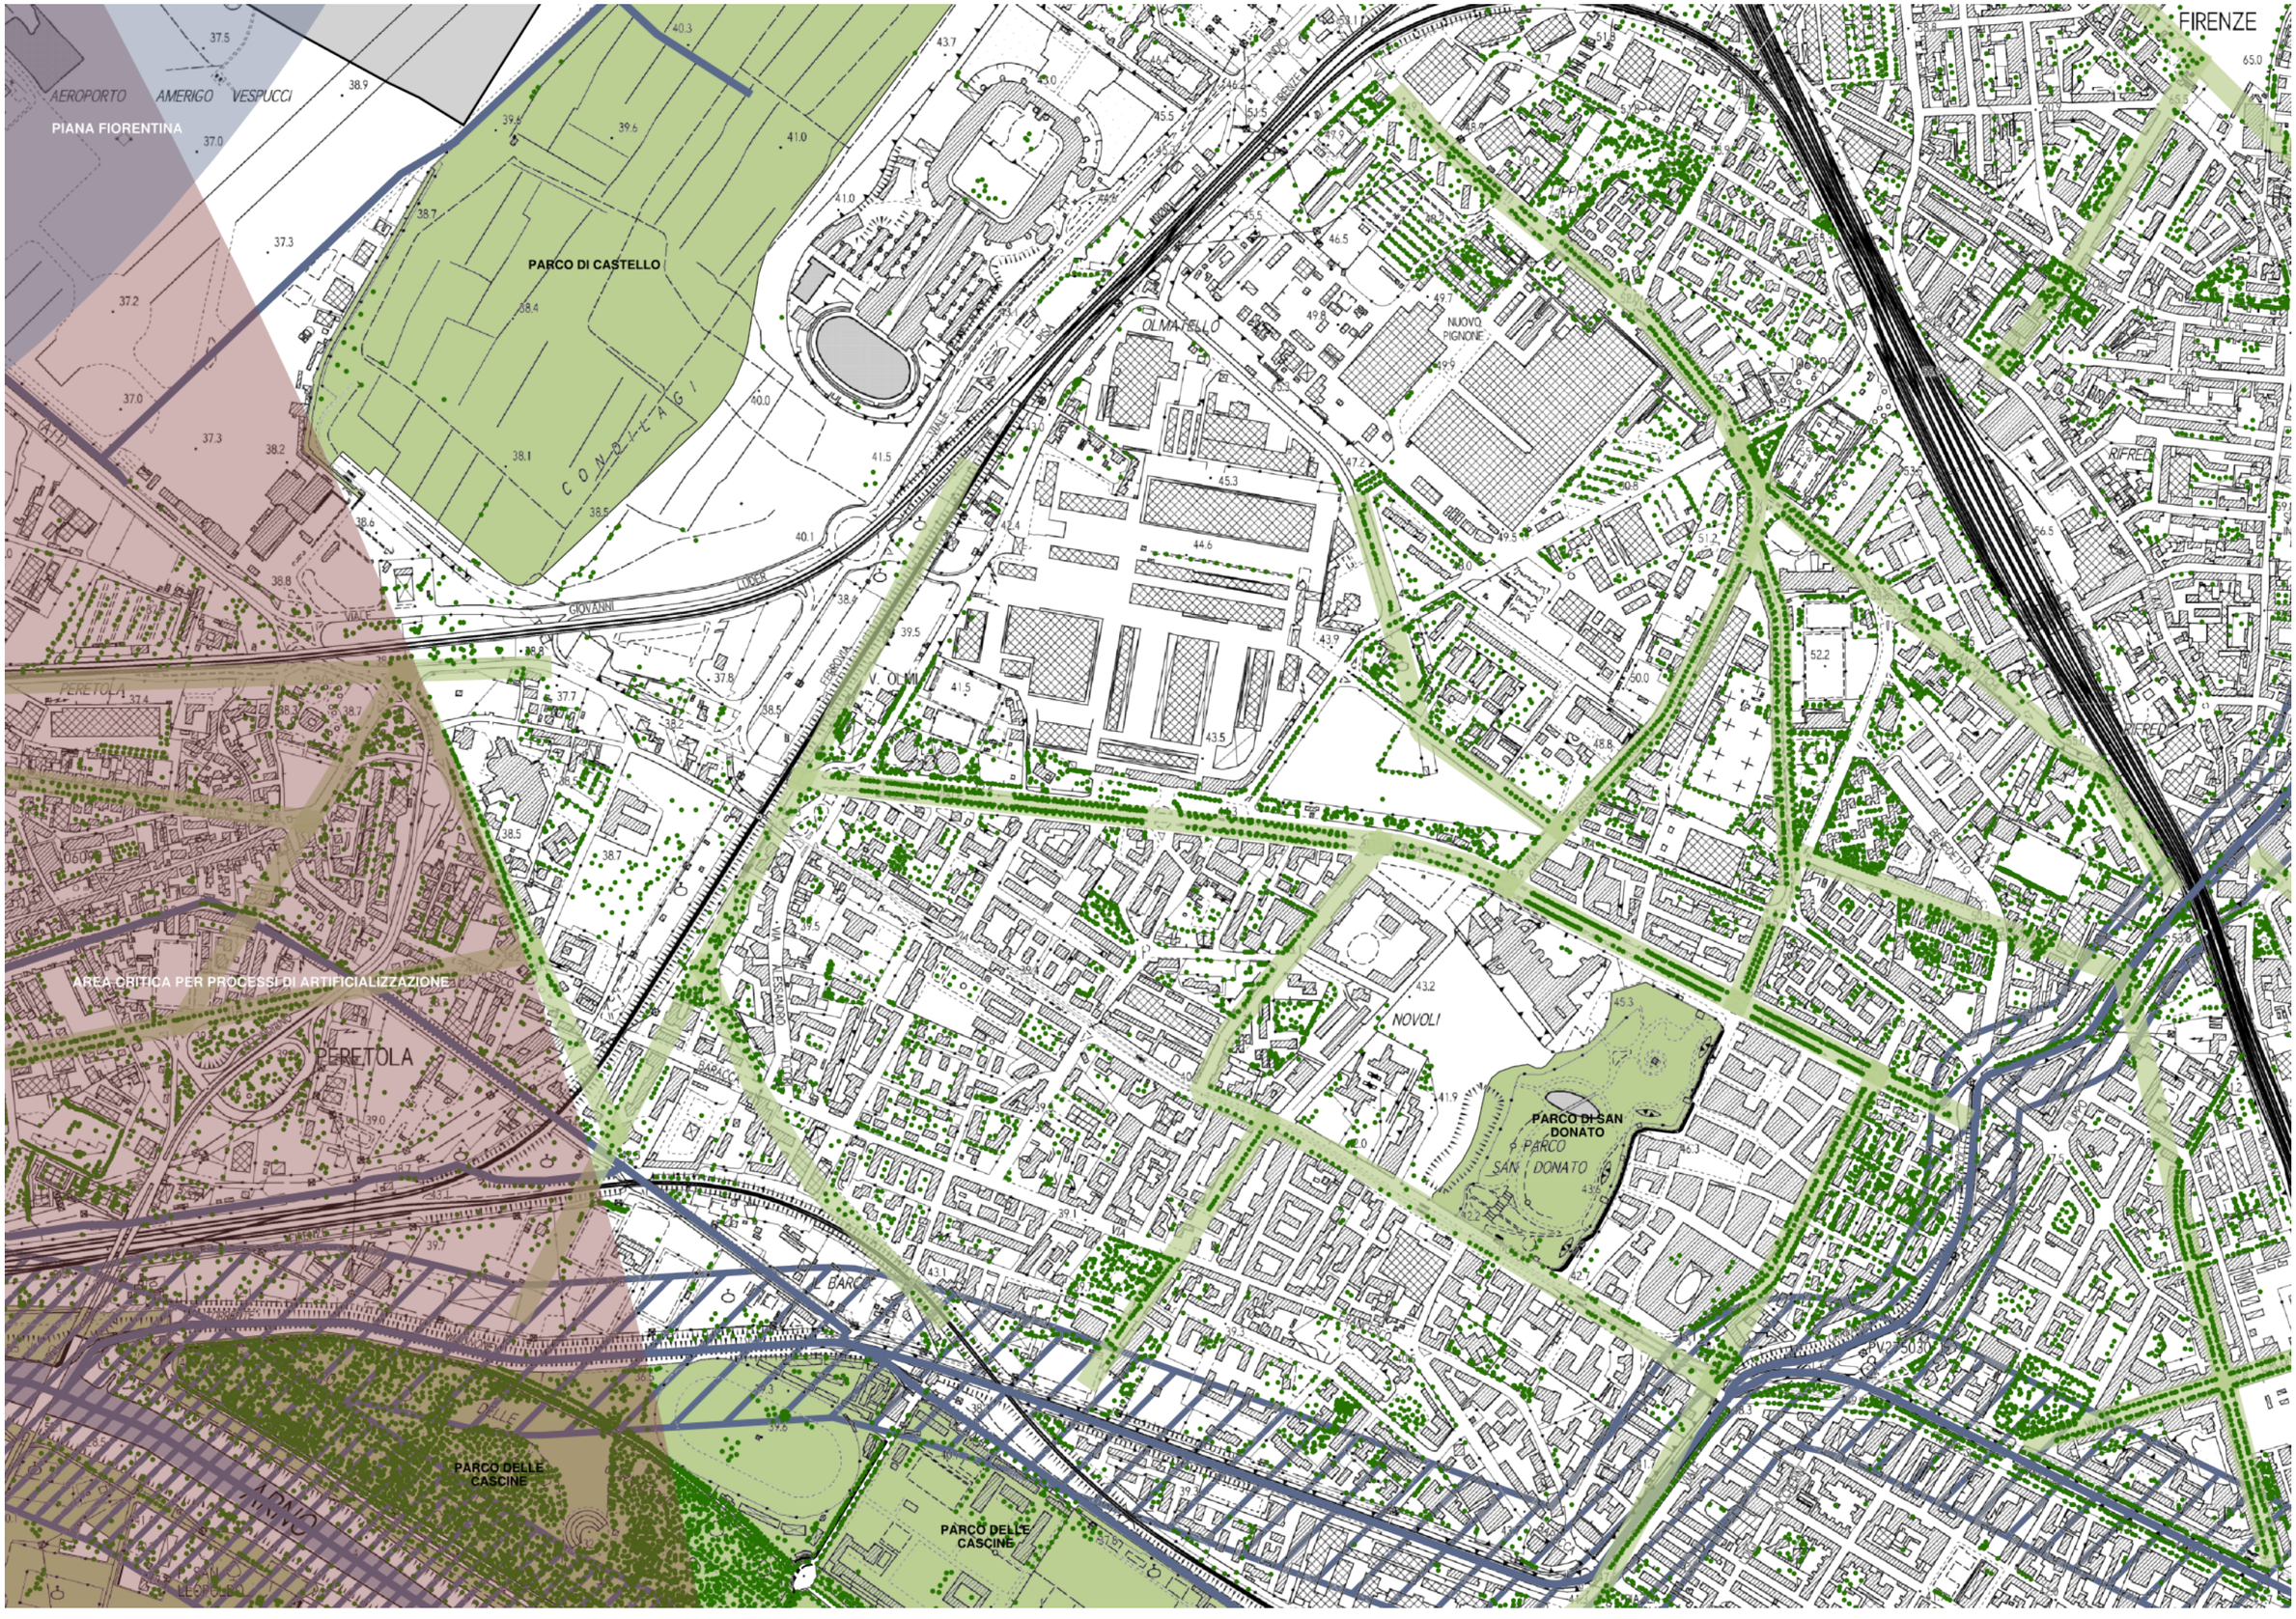

estratto alla data 20 luglio 2025

stampato il 20 luglio 2025

Comune di Firenze - Piano Strutturale

2 | invarianti - scala 1:10.000 - estratto

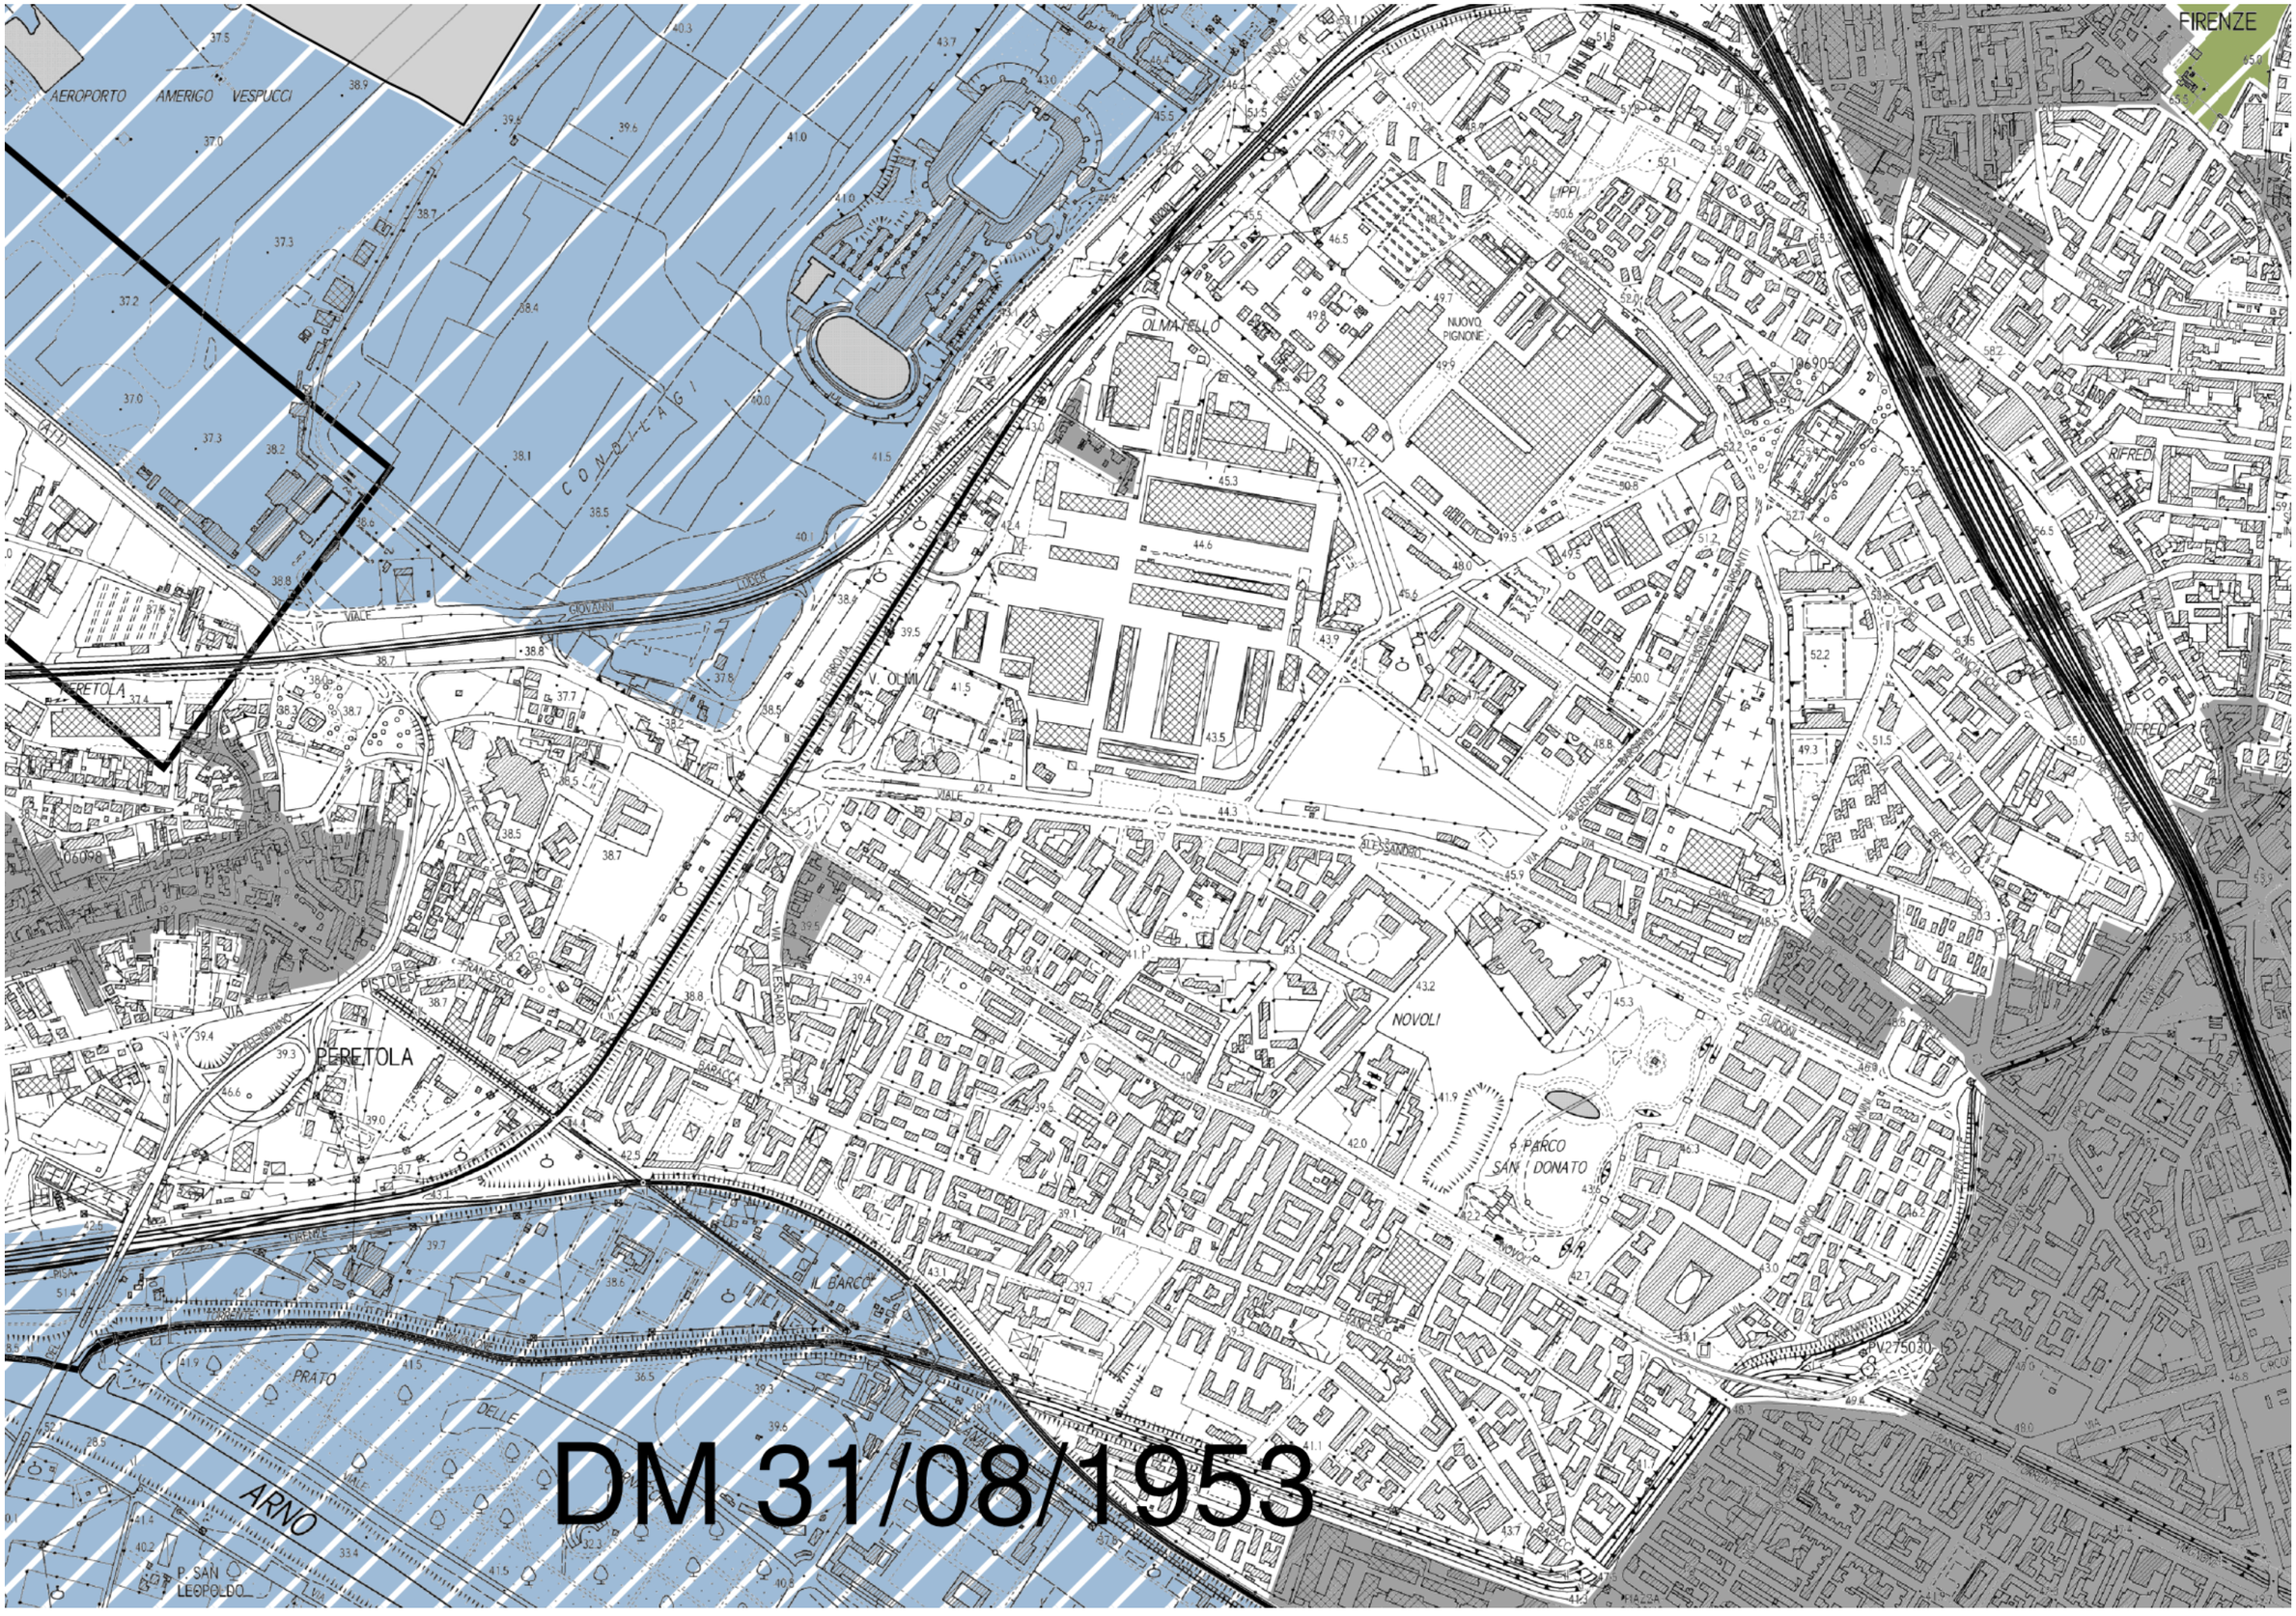

Comune di Firenze - Piano Strutturale

7a | magnitudo idraulica reticolo principale - scala 1:10.000 - estratto

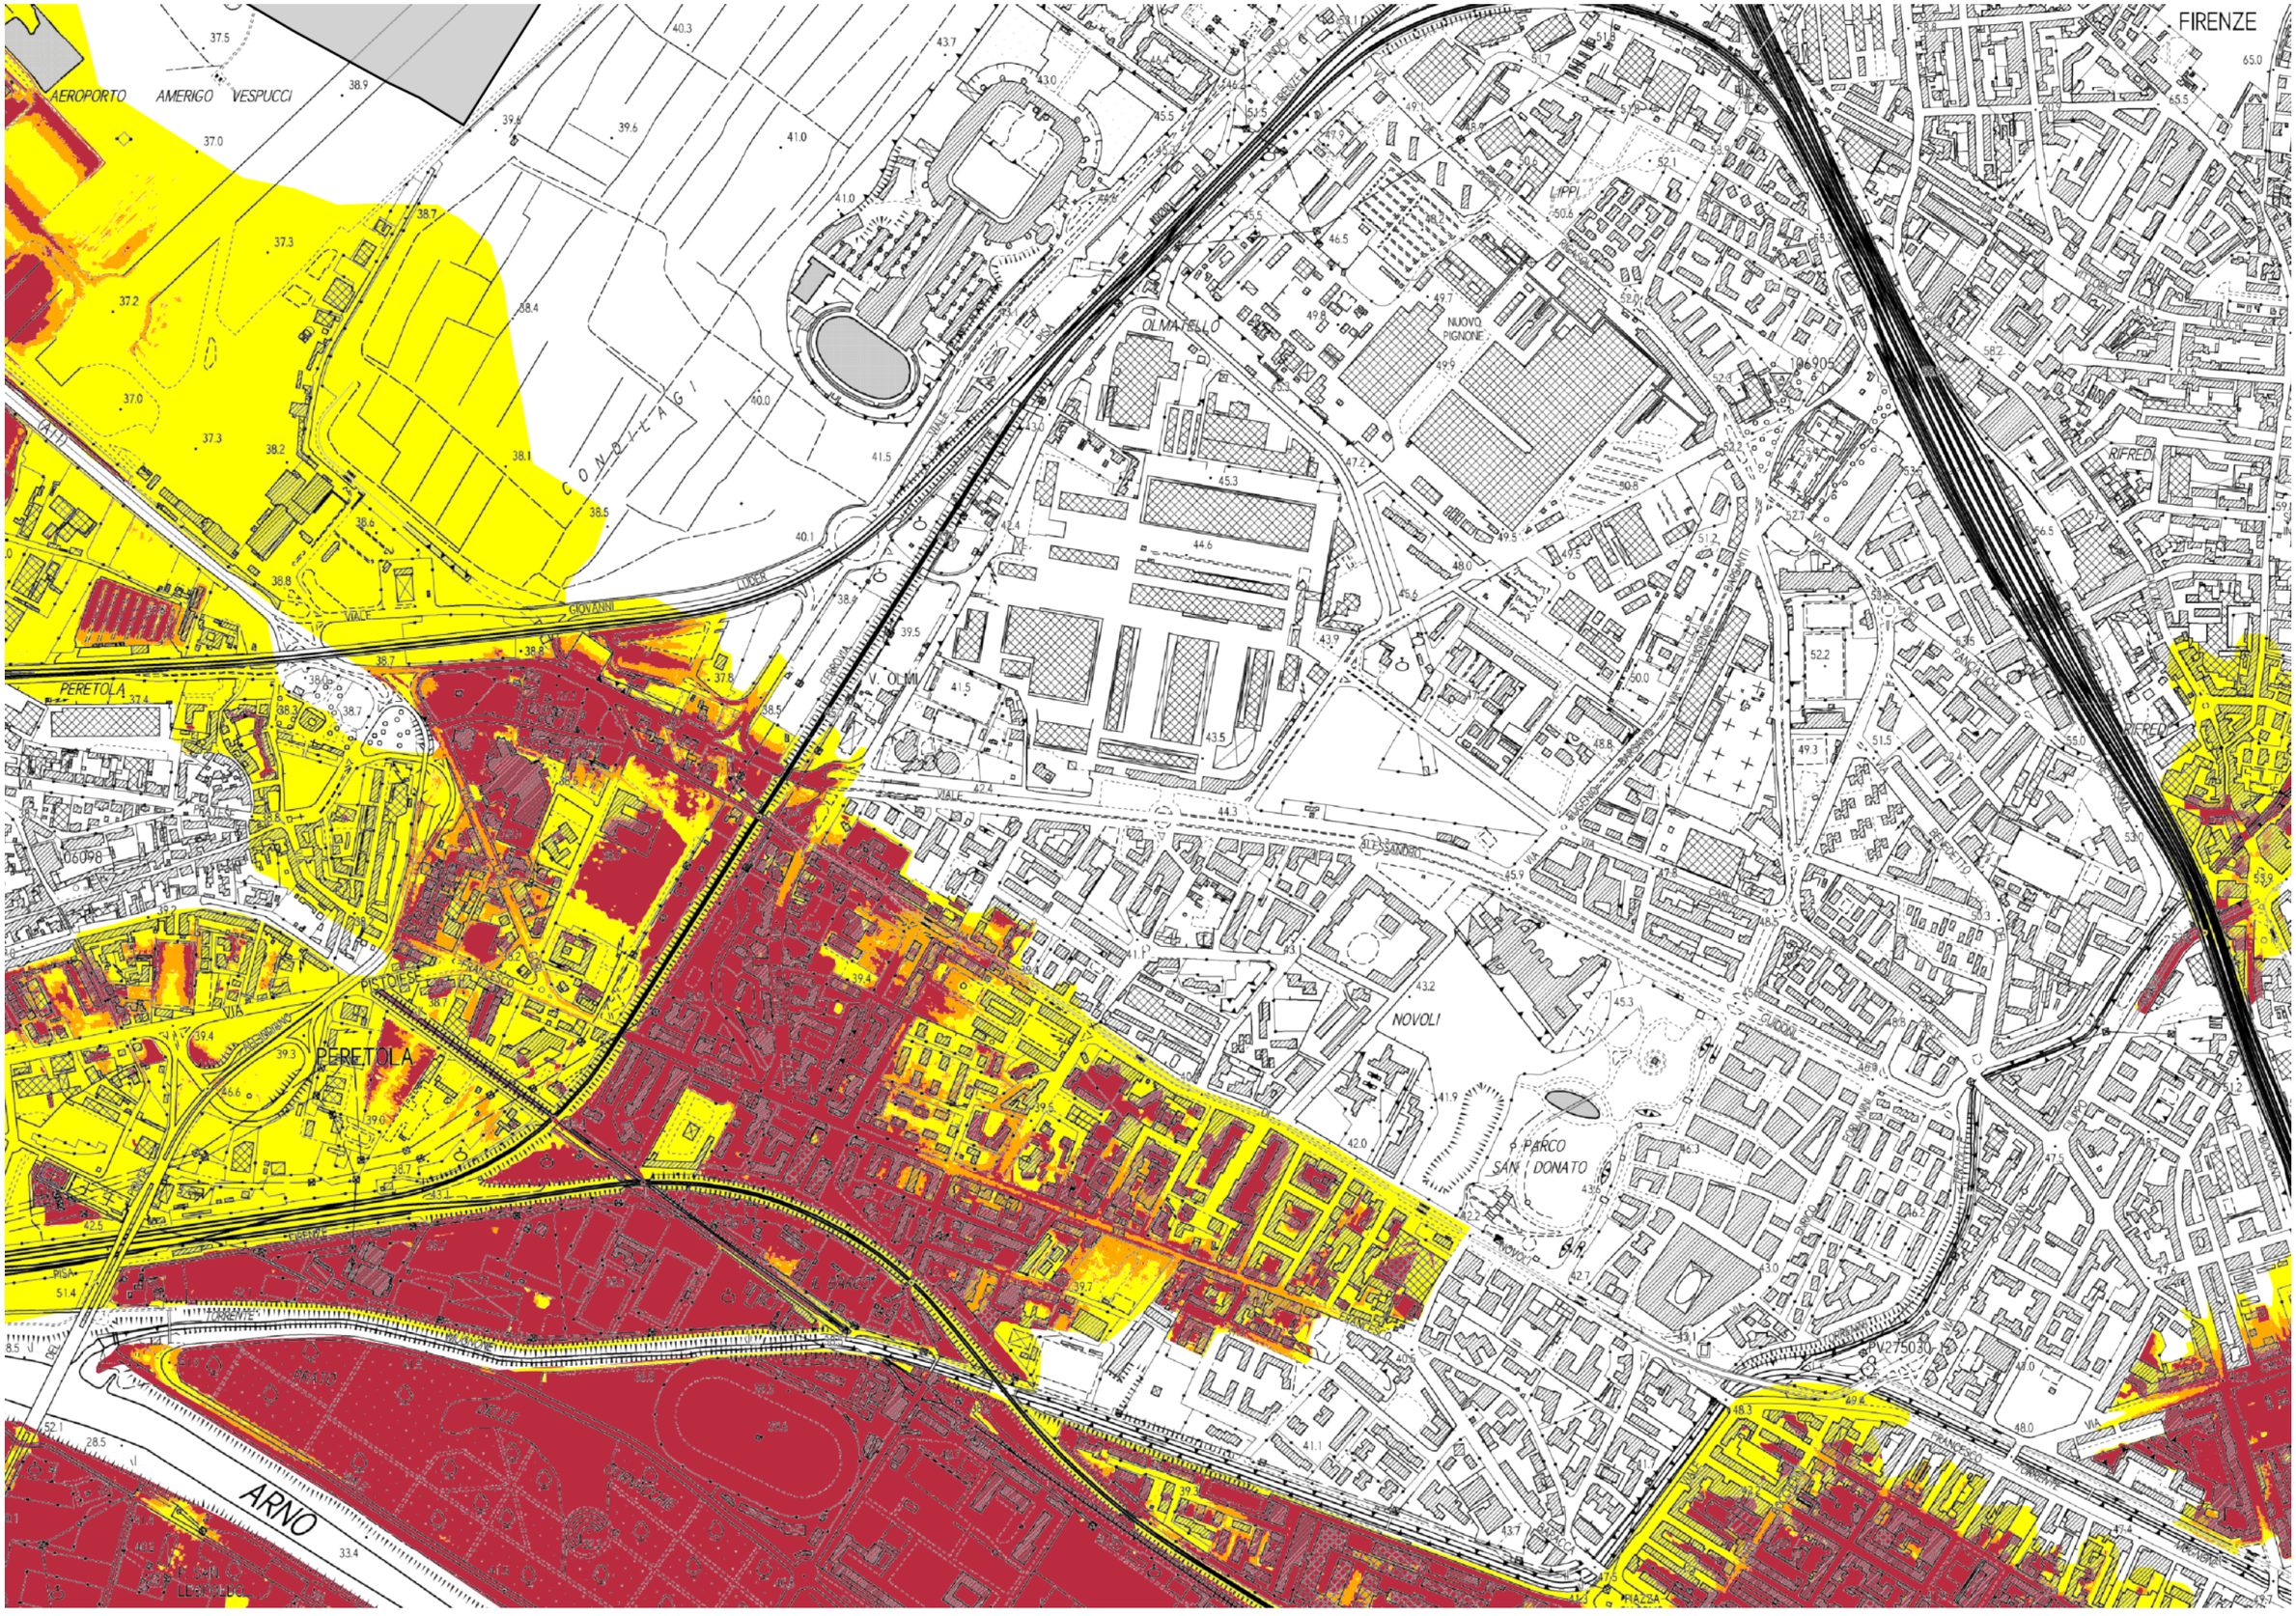

estratto alla data 20 luglio 2025

stampato il 20 luglio 2025

6 | pericolosita' da alluvioni - scala 1:10.000 - estratto

8 | sistema territoriale - scala 1:10.000 - estratto

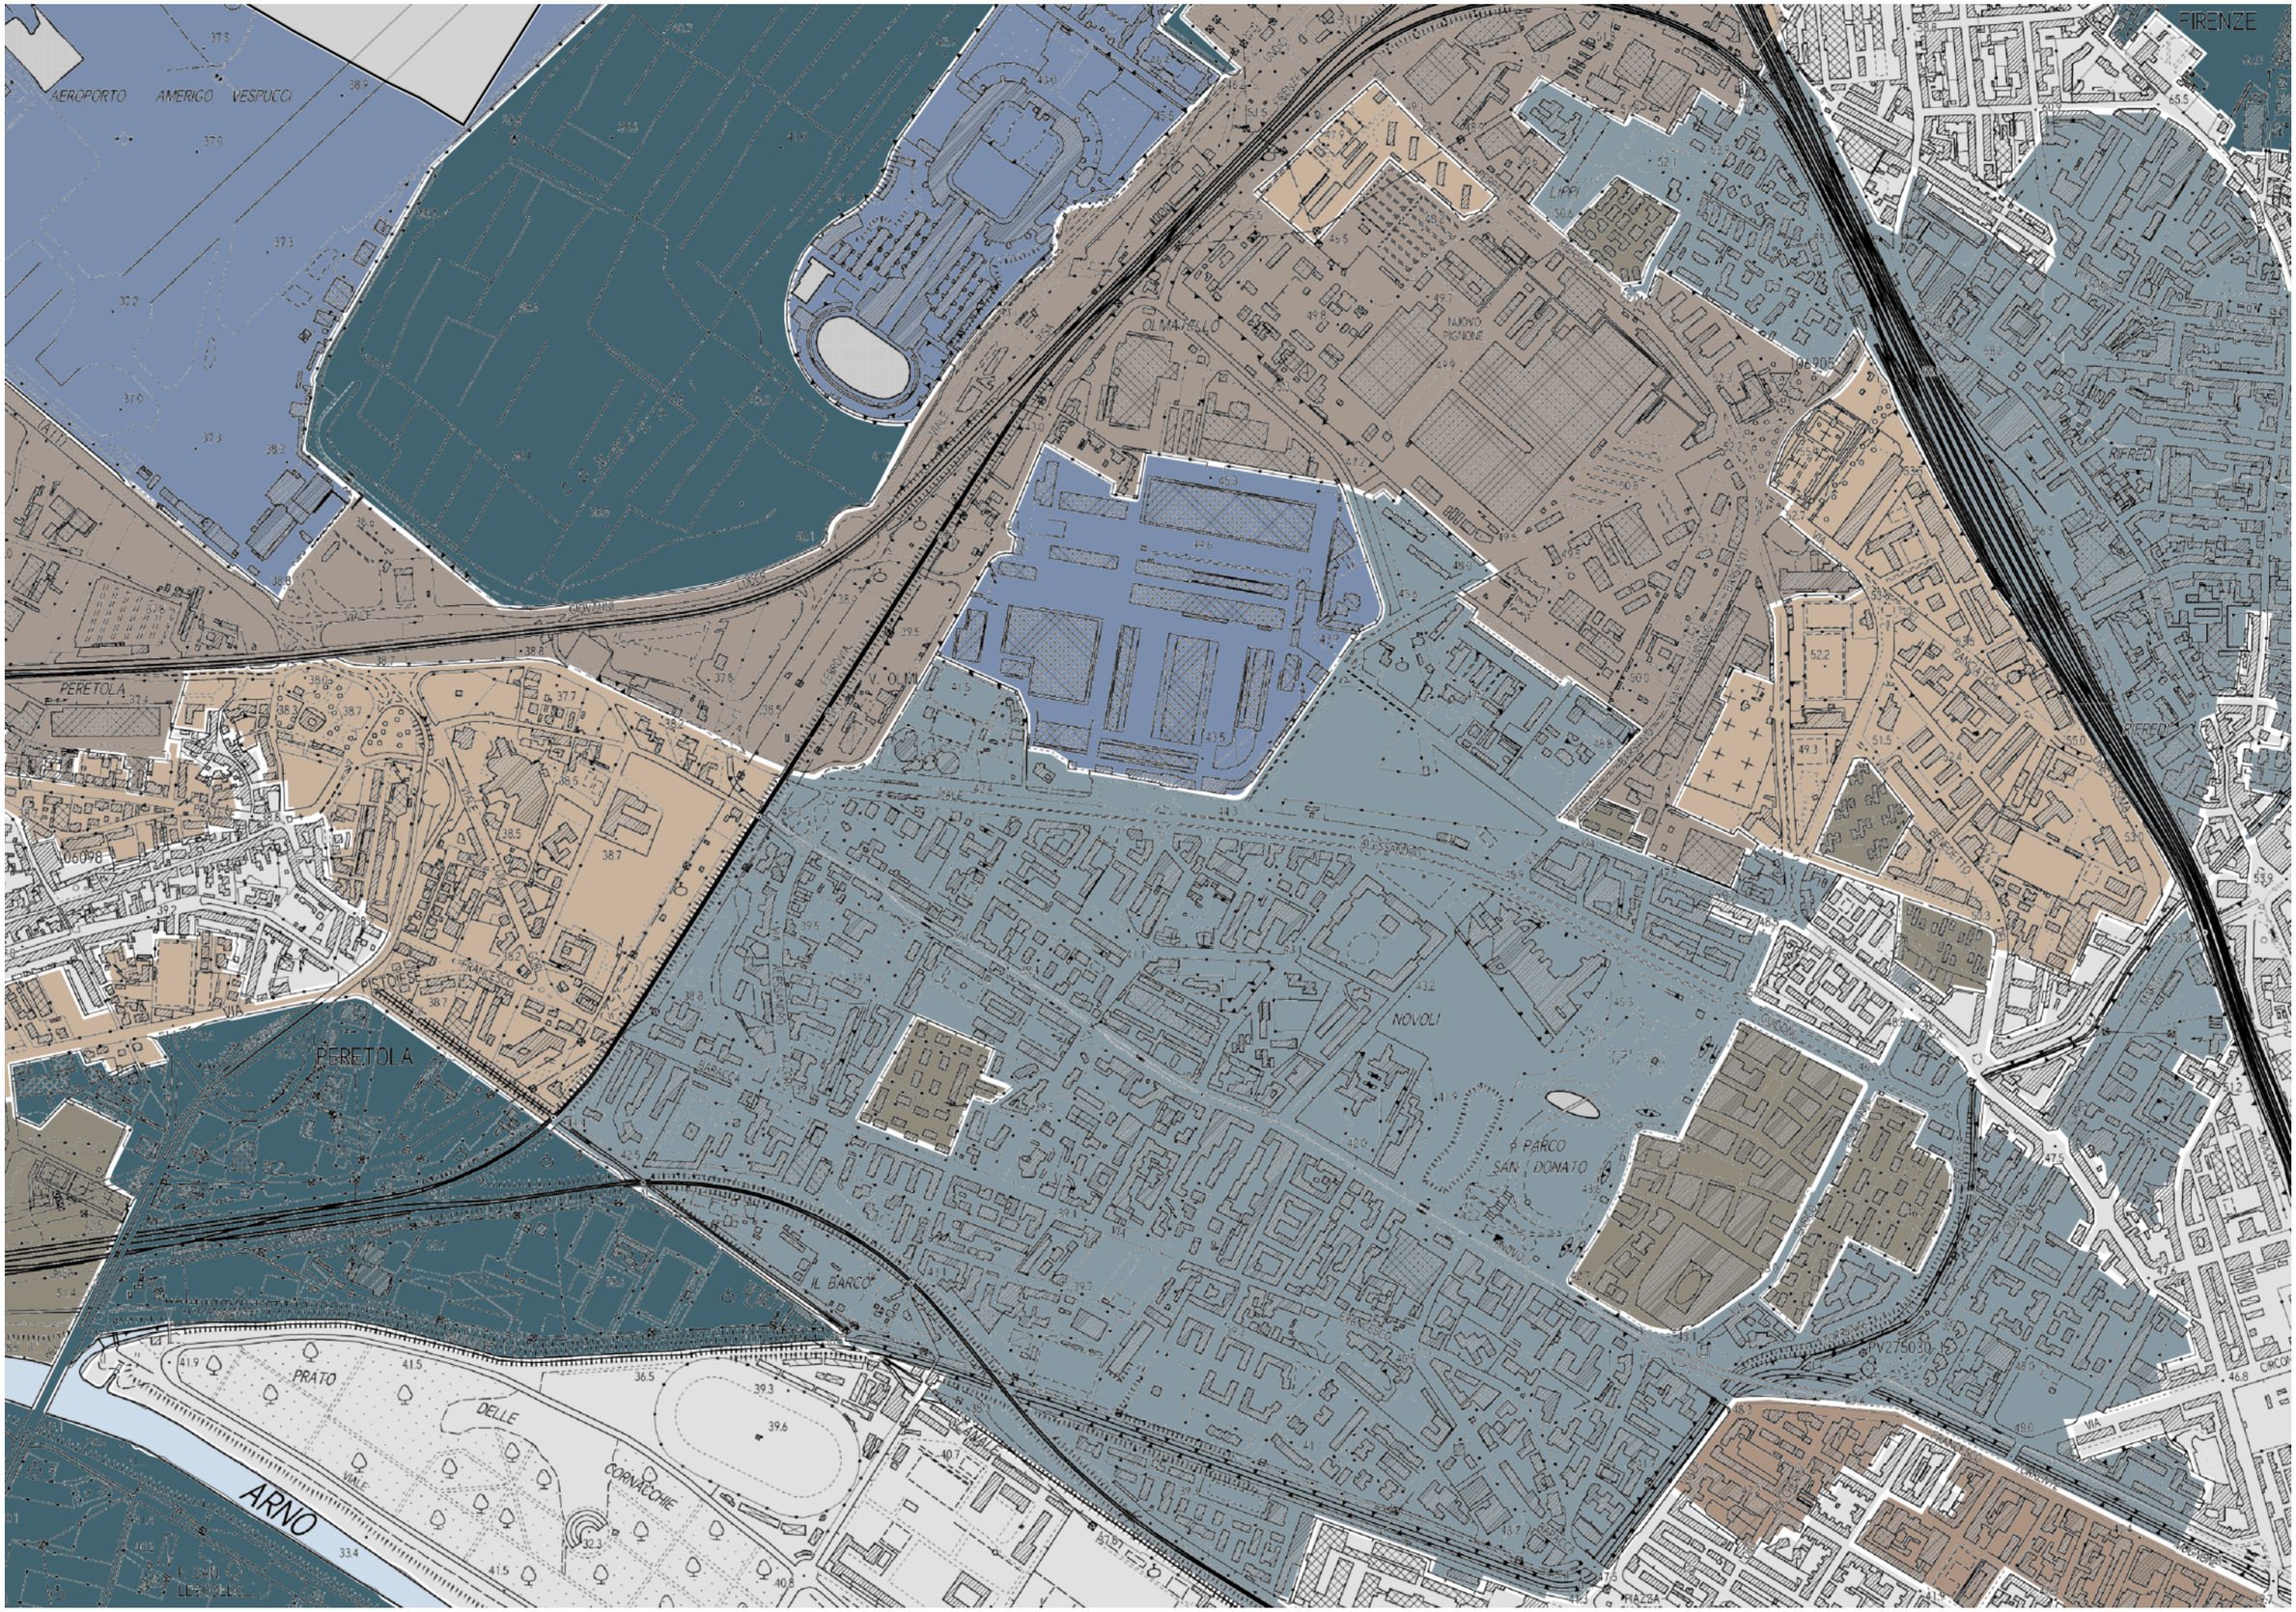

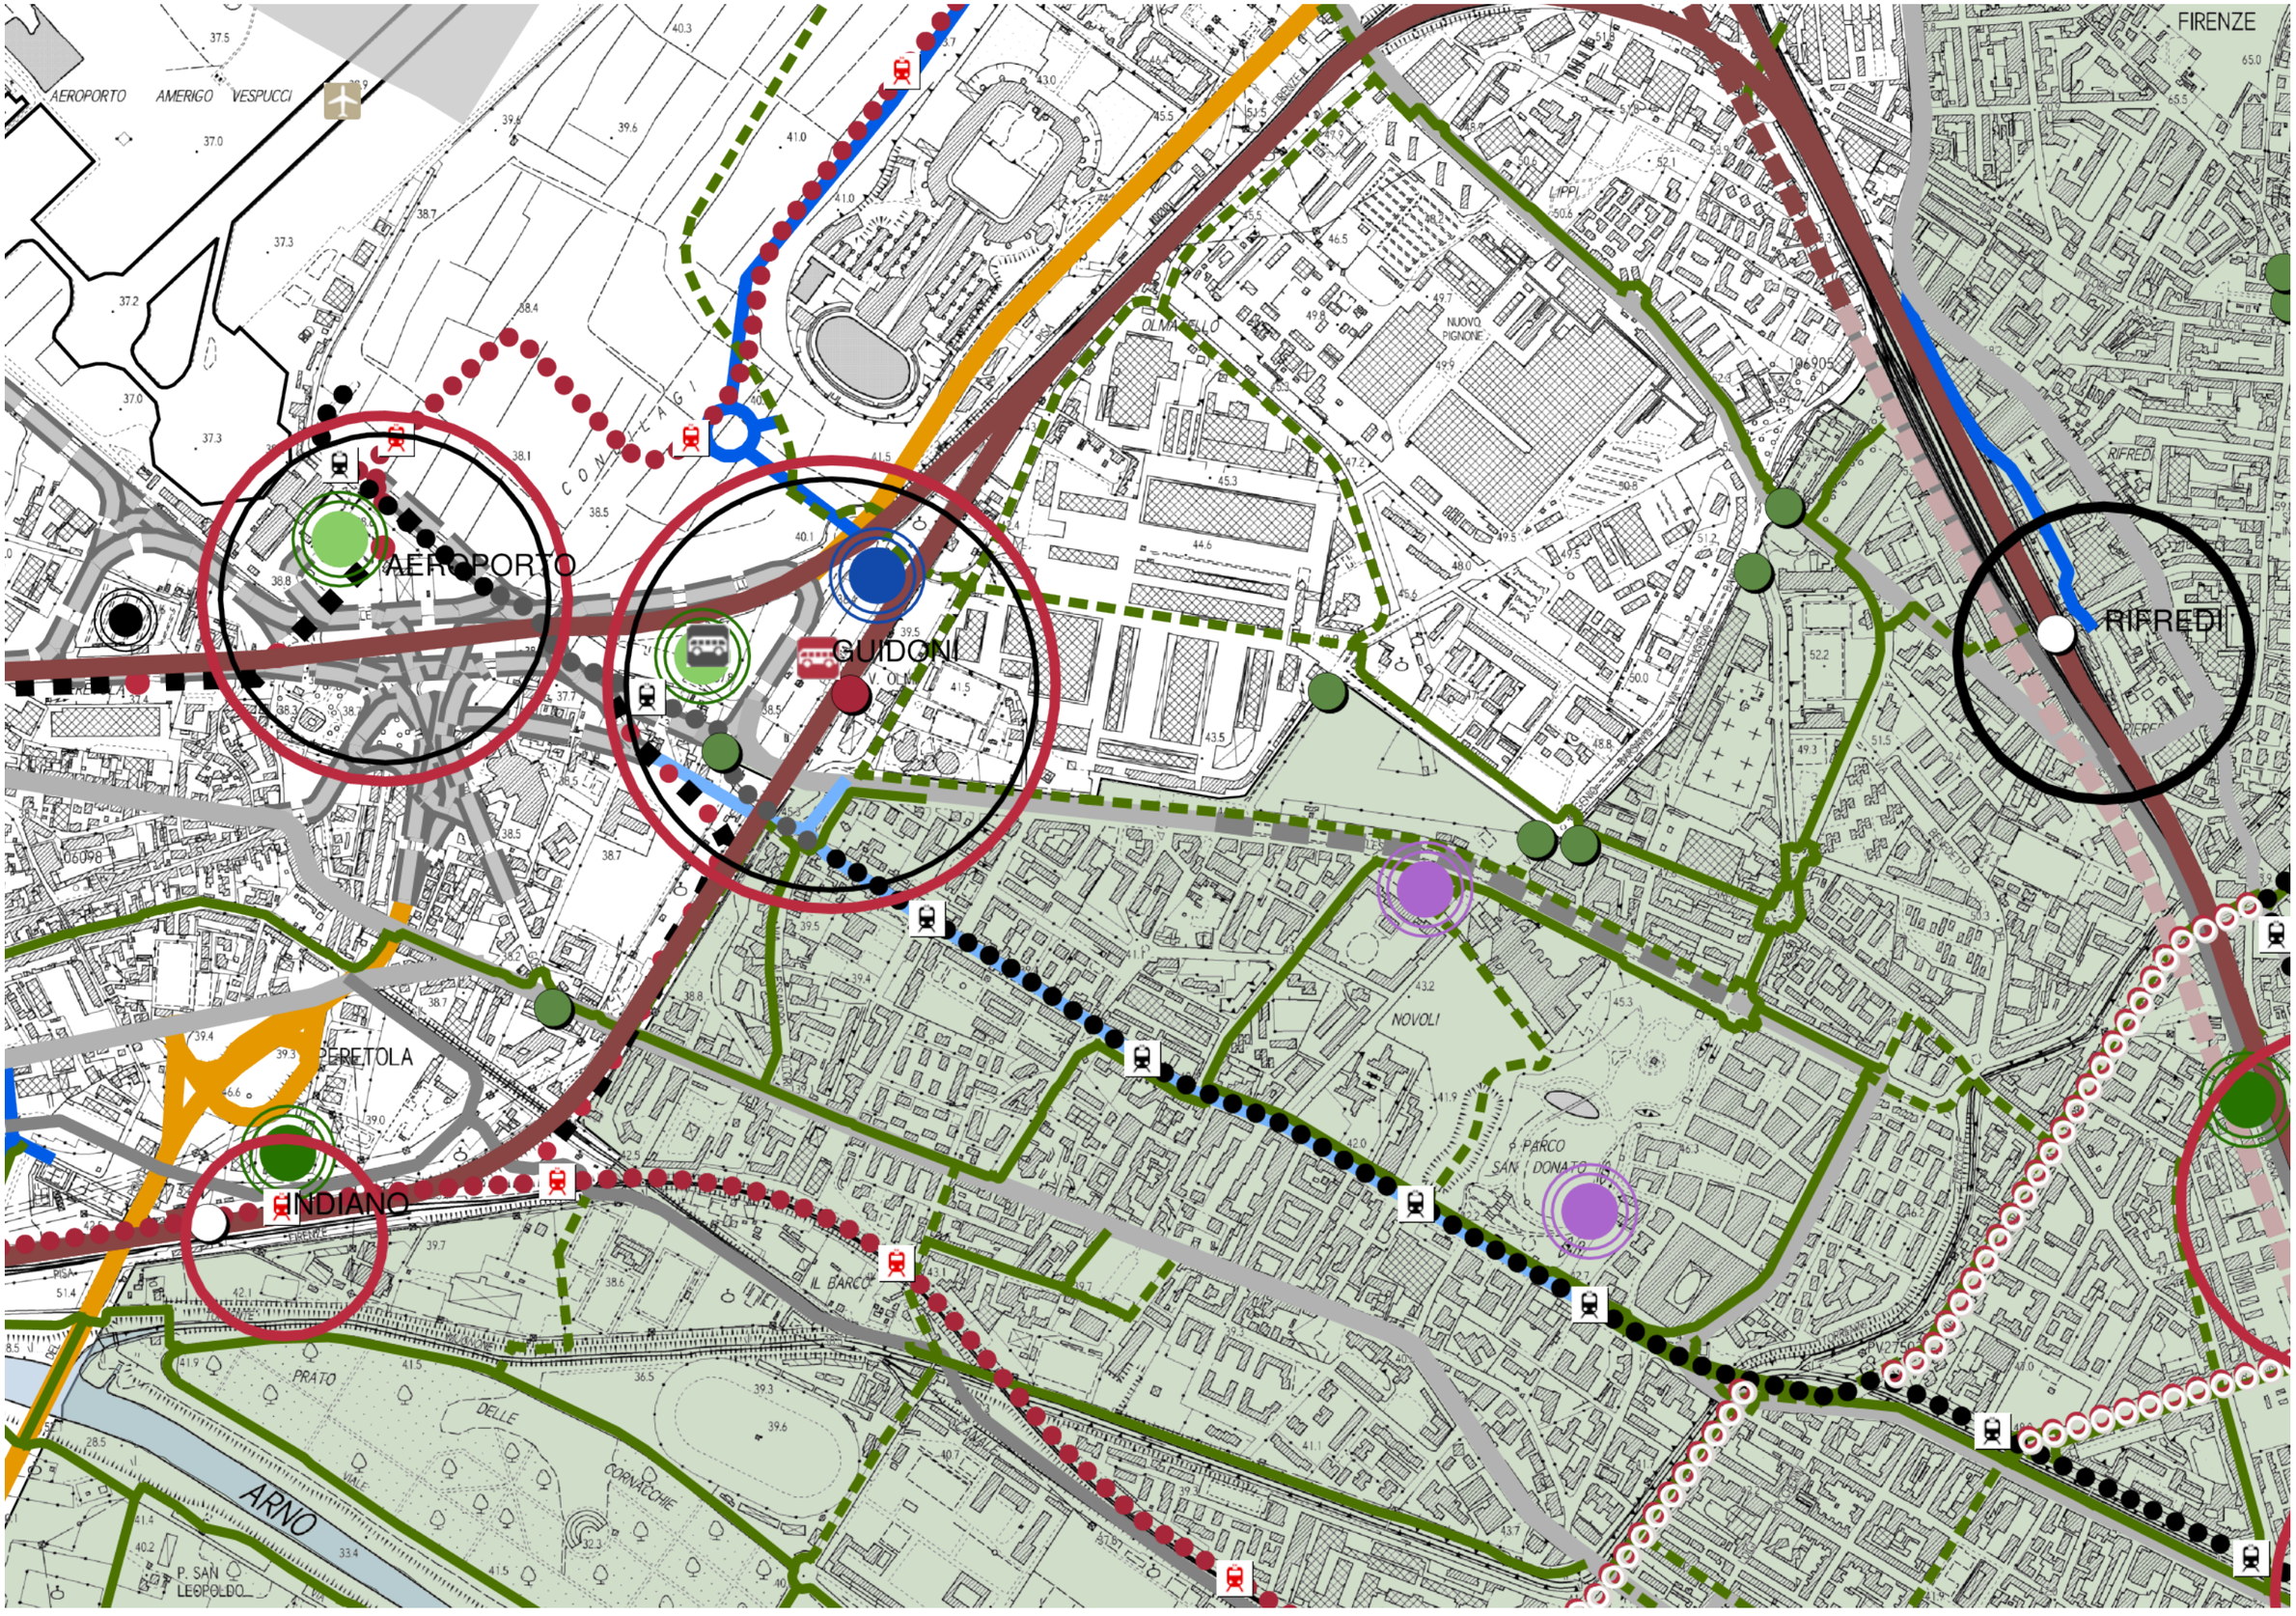
AEROPORTO AMERIGO VESPUCCI
FIRENZE
AEROPORTO
GUIDONI
RIFREDI
INDIANO
PERETOLA
NUOVO PIGNONE
OLMATELLO
LIPPI
NOVOLI
P. PARCO SAN DONATO
IL BARCO
PRATO DELLE CORNACCHIE
ARNO
P. SAN LEOPOLDO

Comune di Firenze - Piano Strutturale

1 | vincoli - scala 1:10.000 - estratto

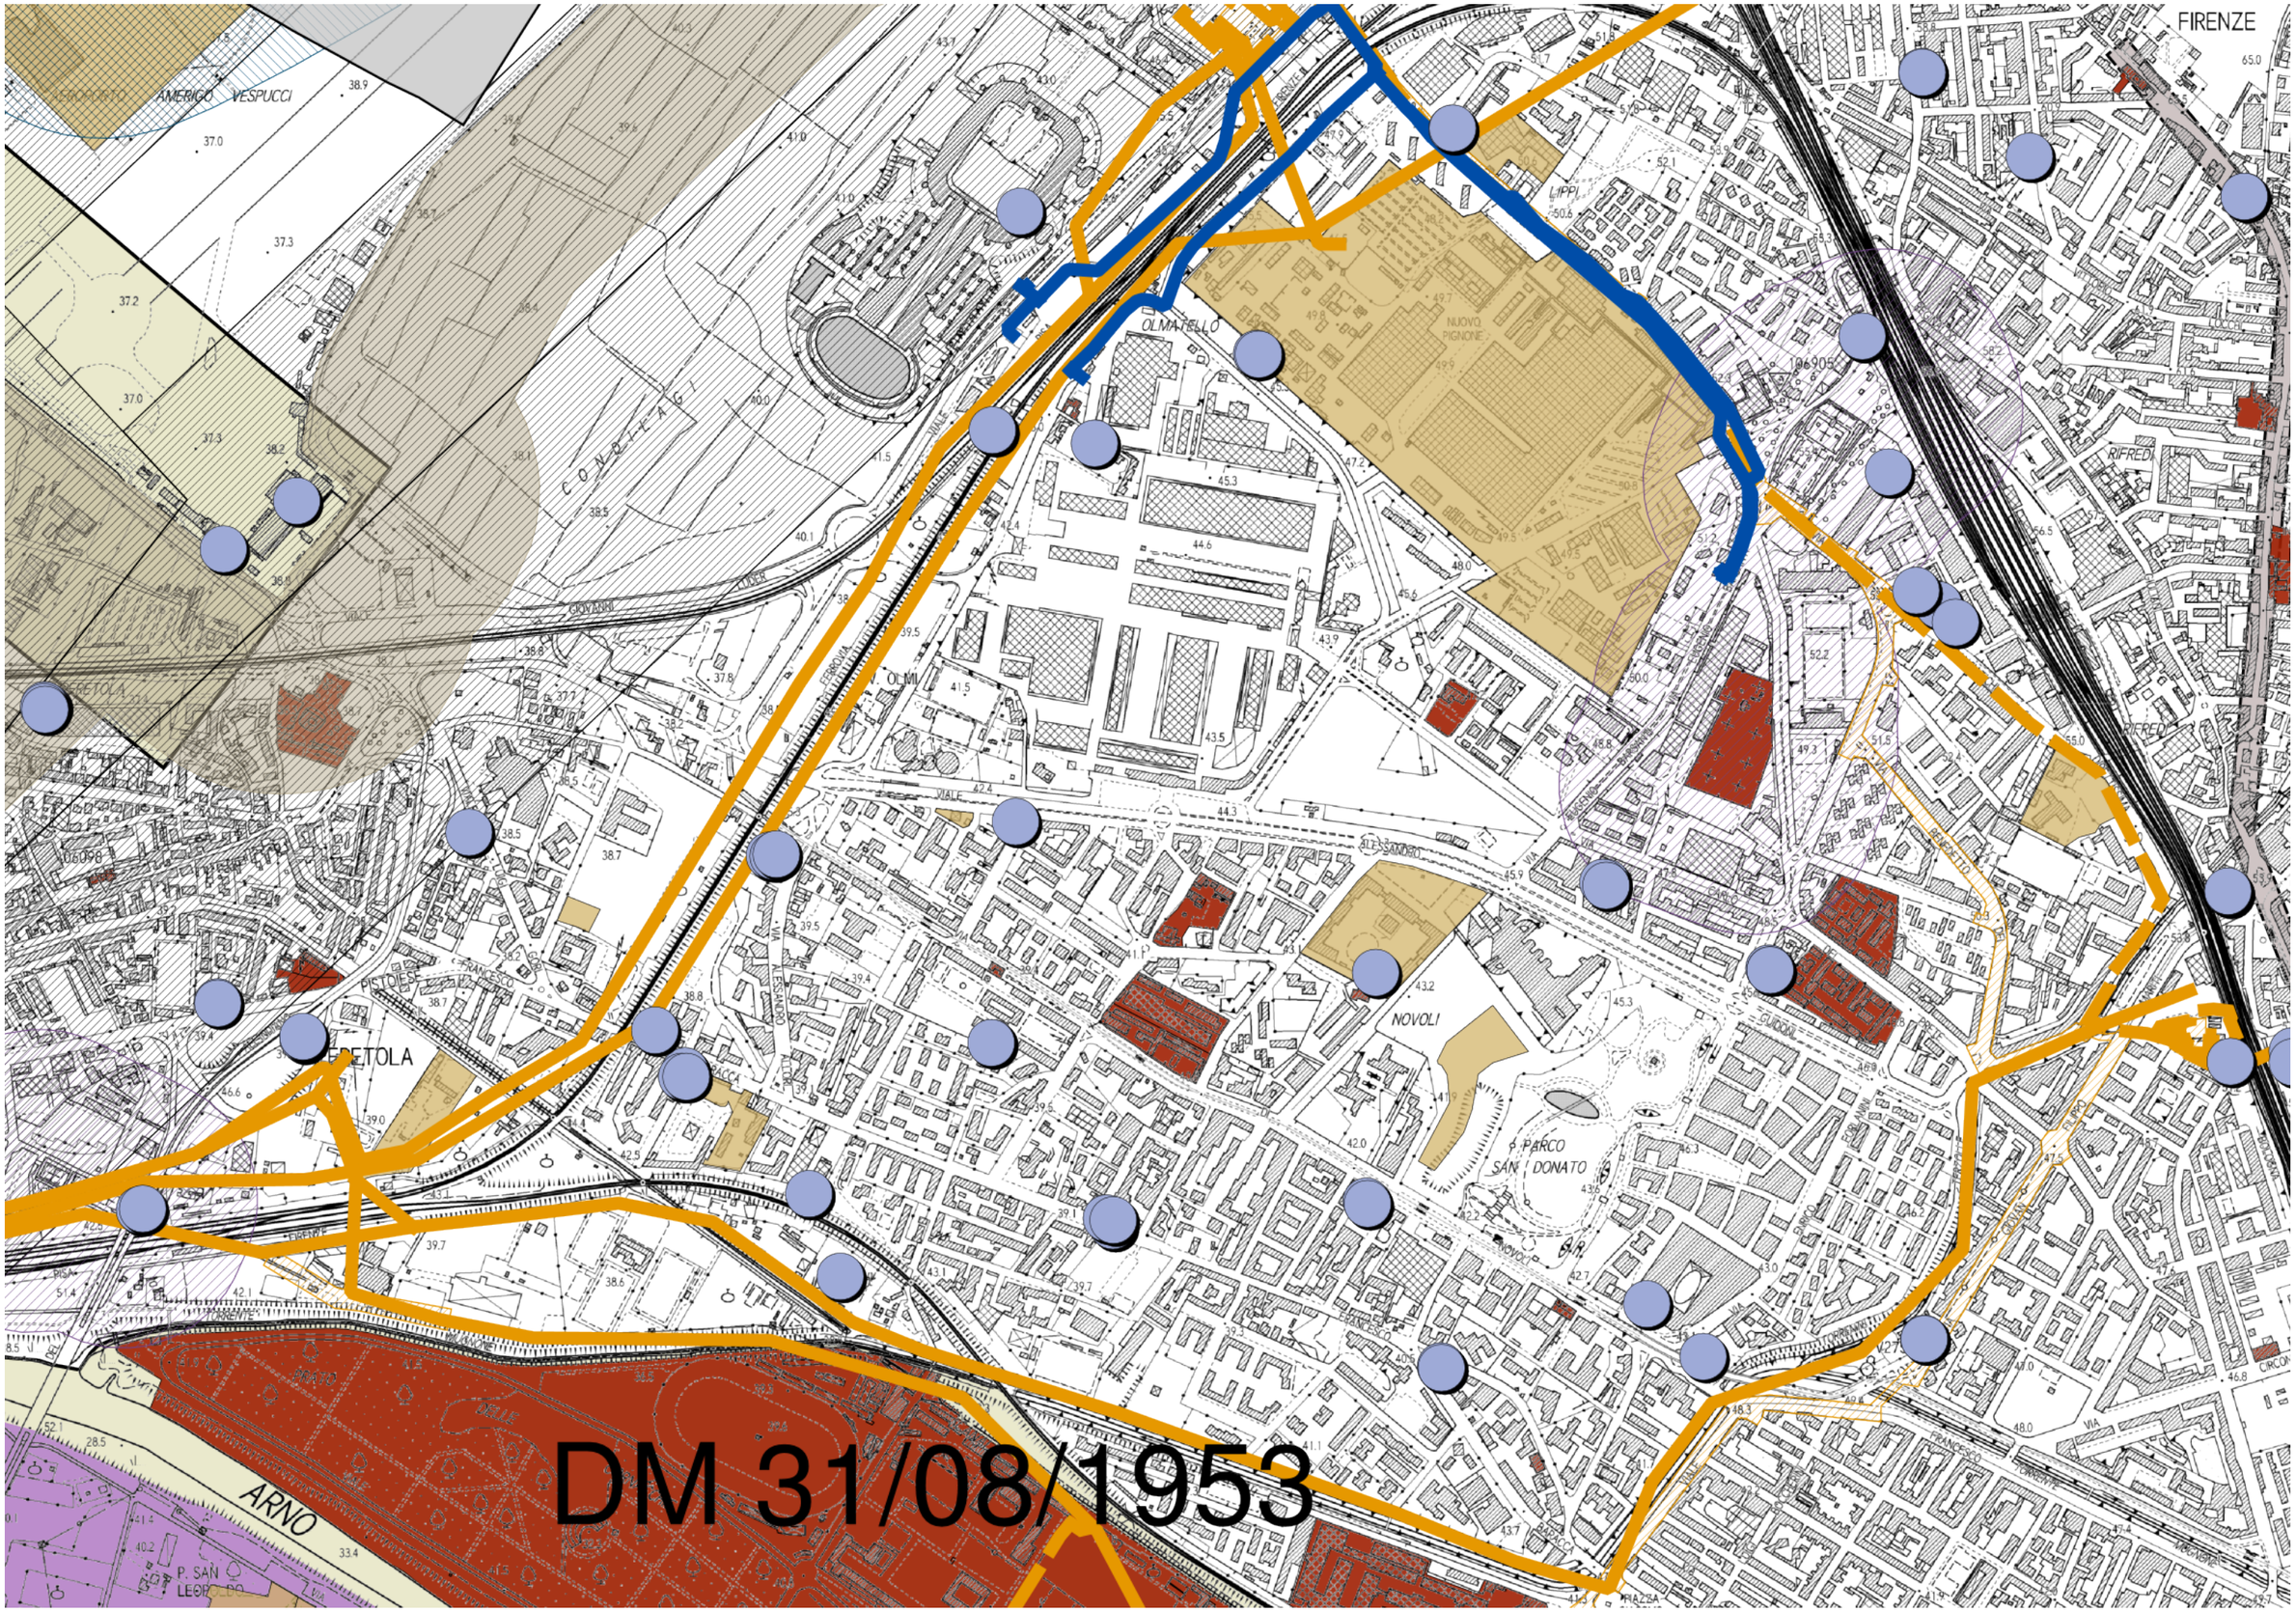

estratto alla data 20 luglio 2025

stampato il 20 luglio 2025