Comune di Firenze - Piano Operativo

disciplina del suolo e degli insediamenti - scala 1:5.000 - estratto

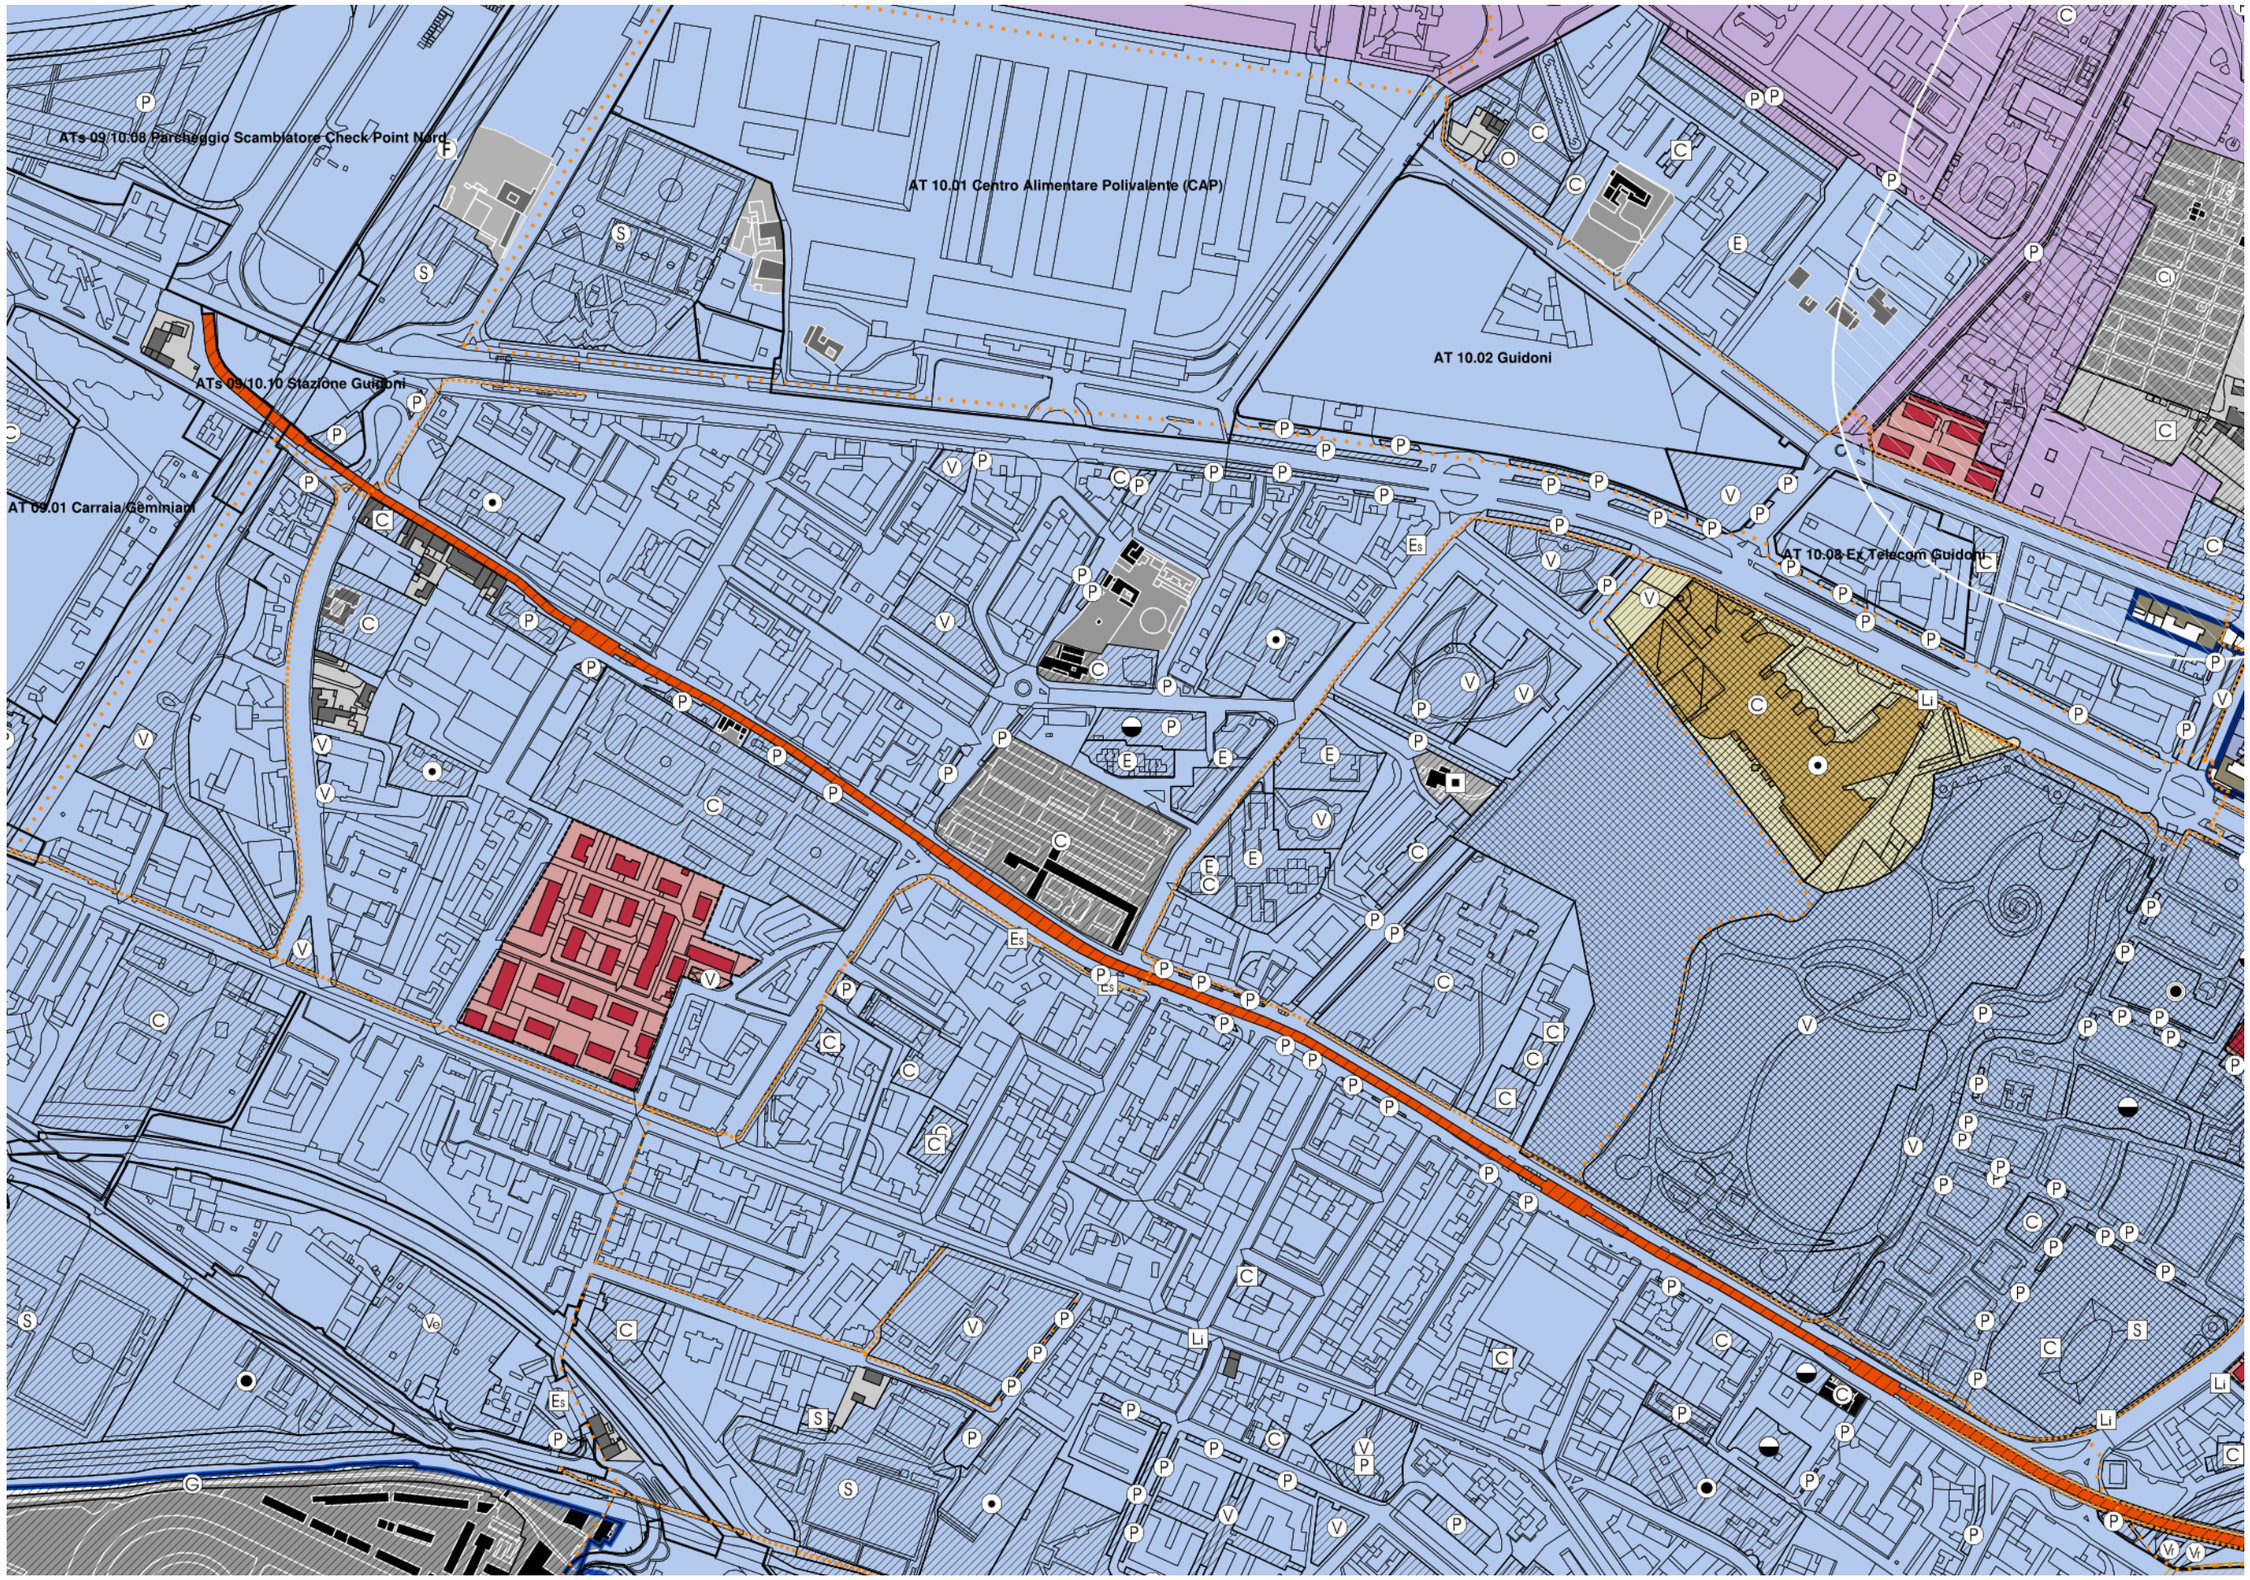

estratto alla data 20 luglio 2025

stampato il 20 luglio 2025

Comune di Firenze - Piano Strutturale

11 | attrezzature e spazi collettivi - scala 1:10.000 - estratto

estratto alla data 20 luglio 2025

stampato il 20 luglio 2025

9 | dotazioni ecologico ambientali - scala 1:10.000 - estratto

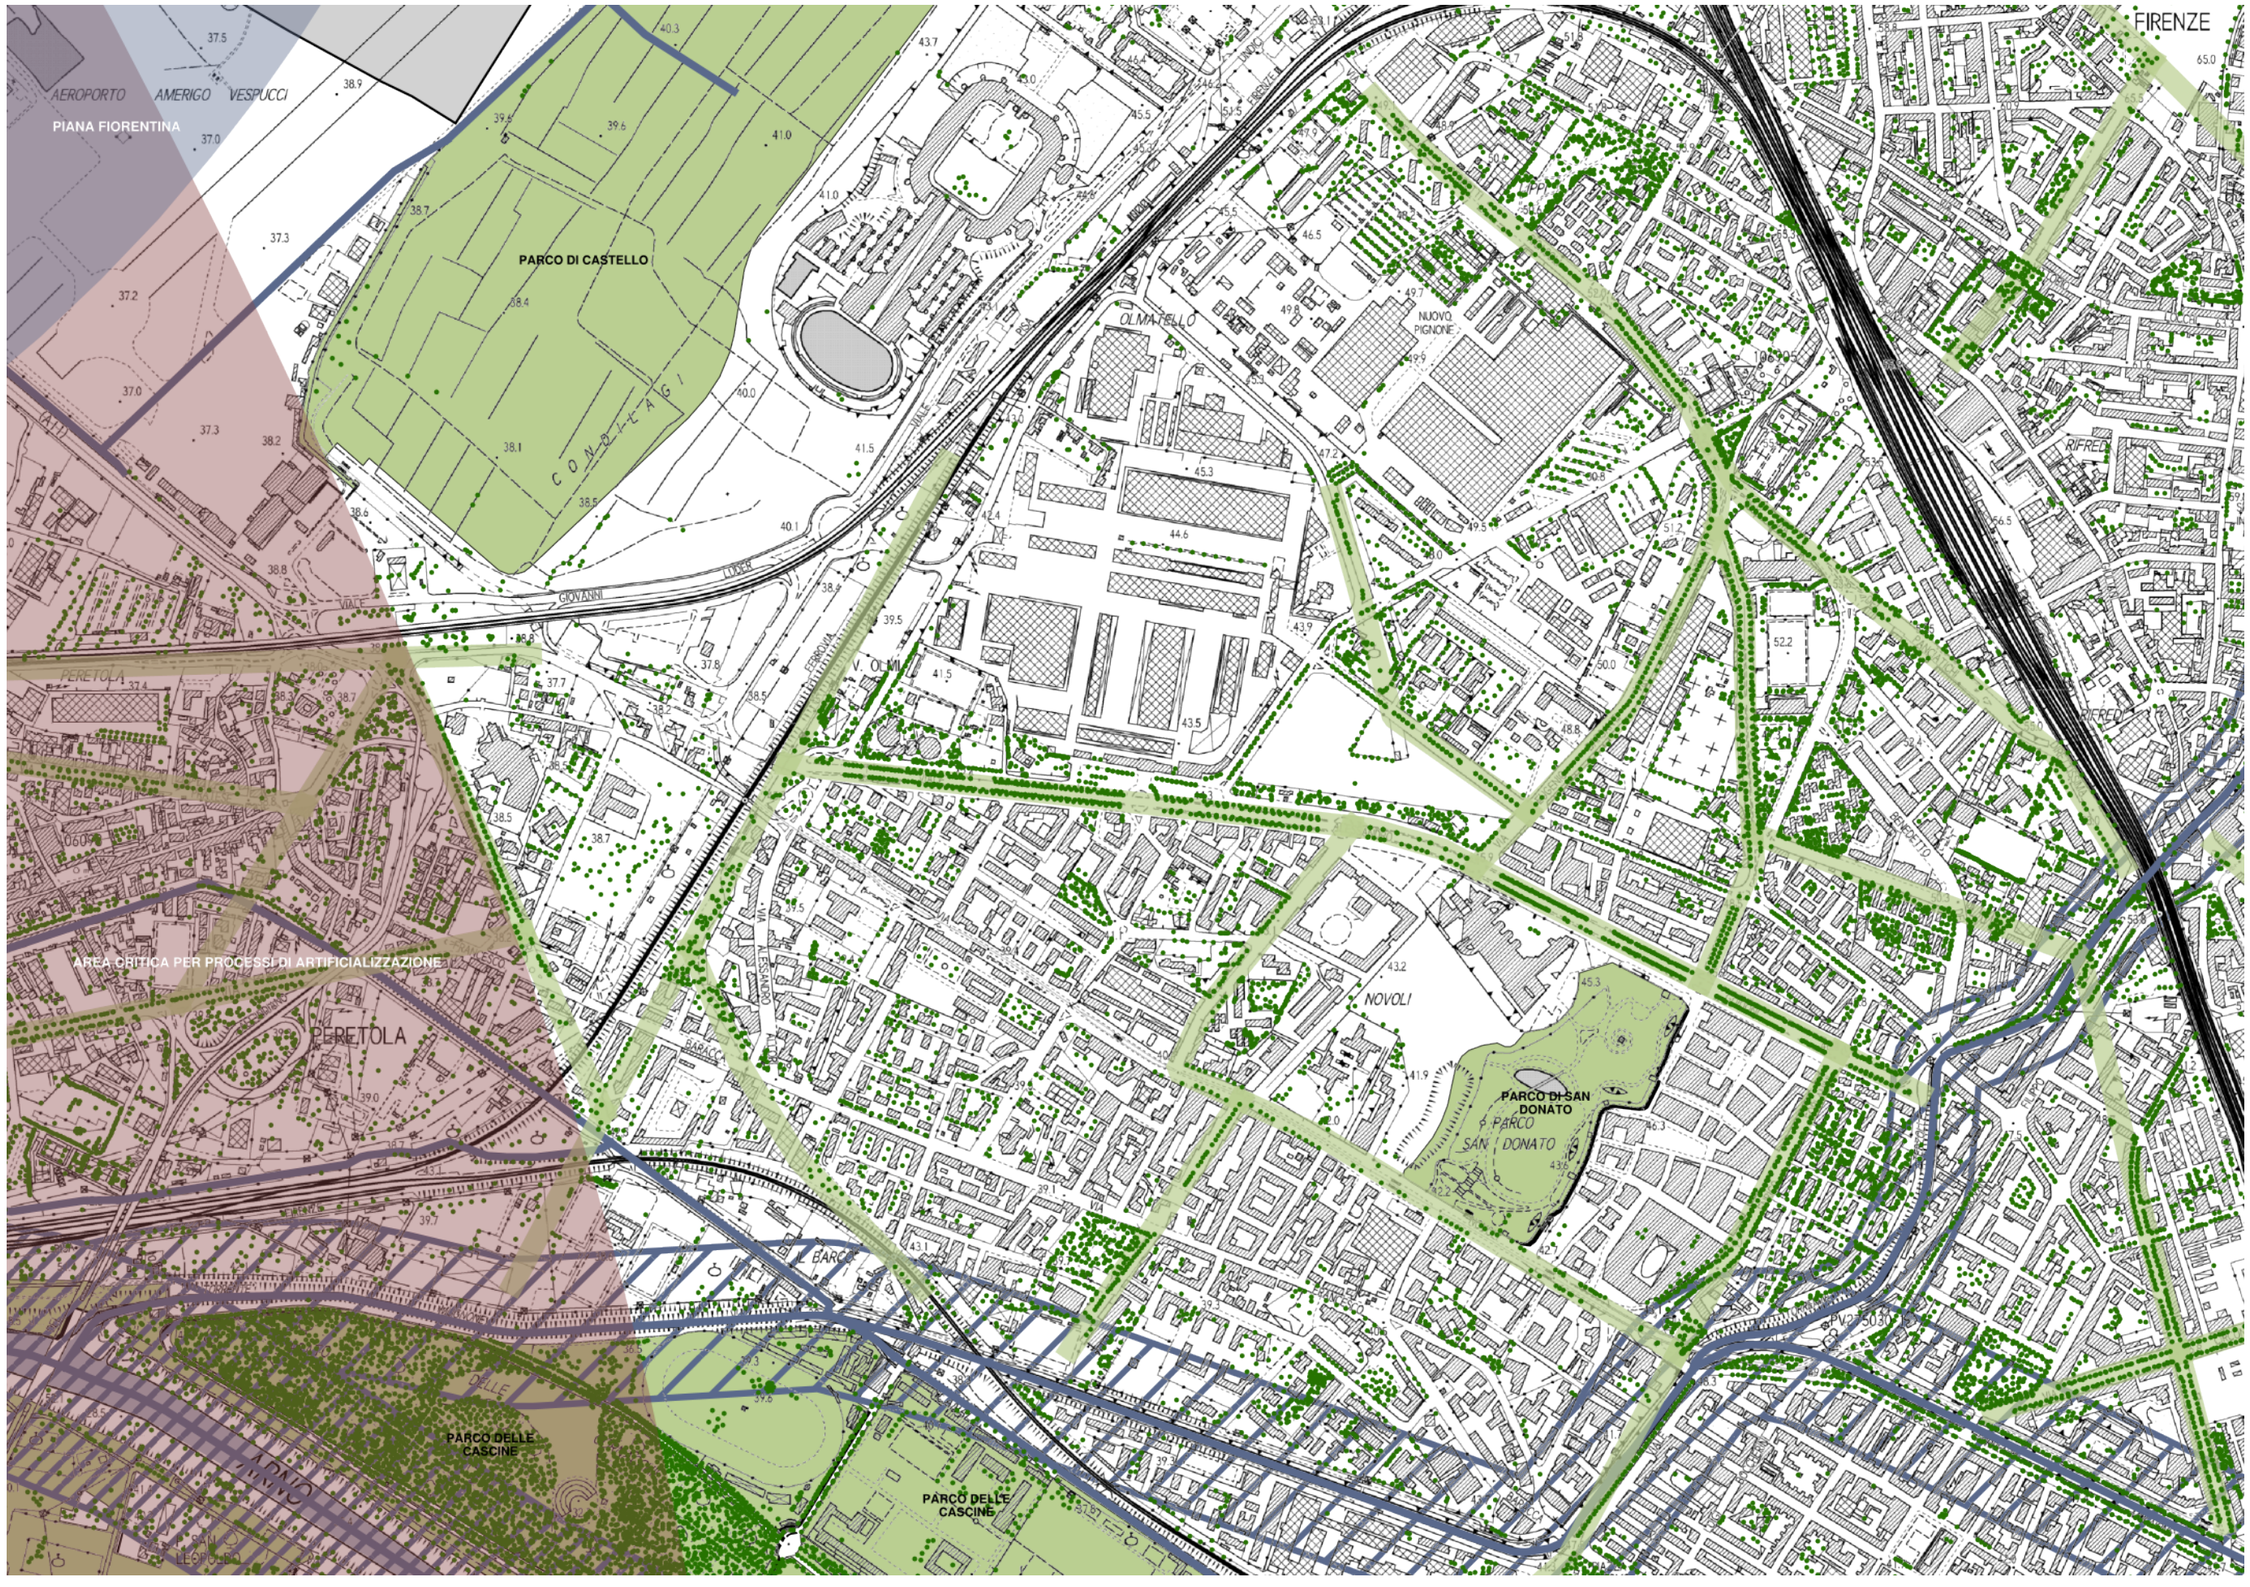

Comune di Firenze - Piano Strutturale

2 | invarianti - scala 1:10.000 - estratto

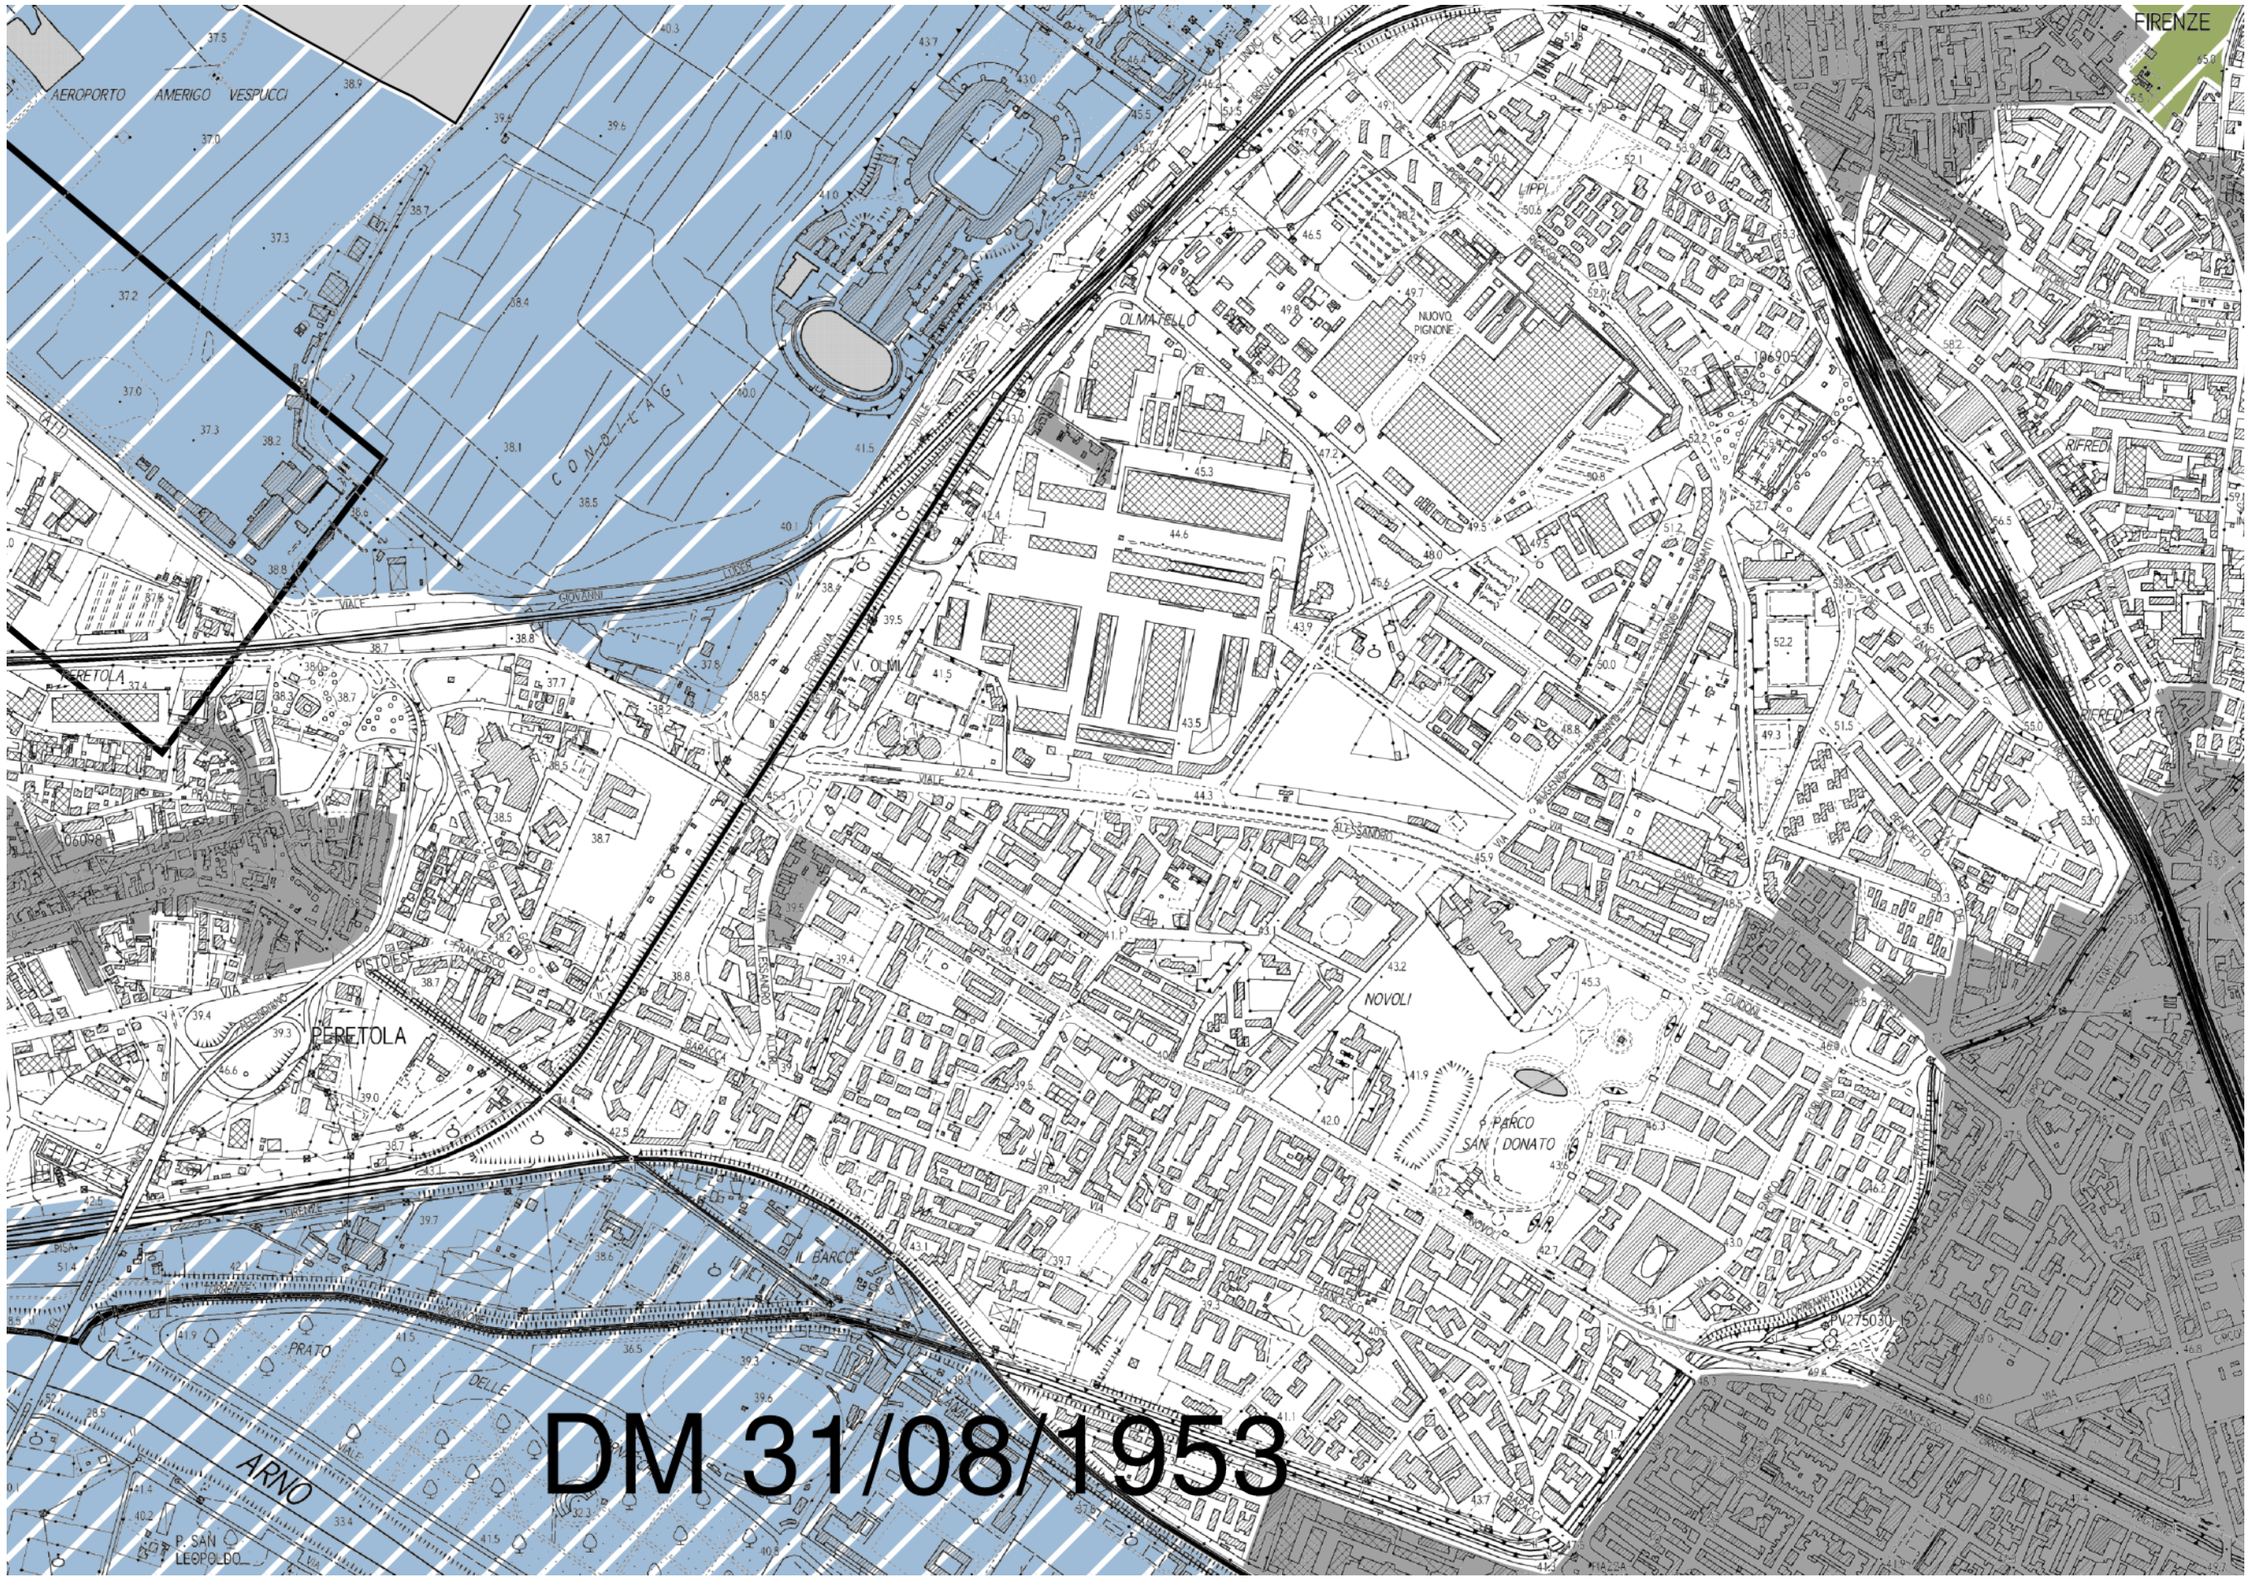

estratto alla data 20 luglio 2025

stampato il 20 luglio 2025

Comune di Firenze - Piano Strutturale

7a | magnitudo idraulica reticolo principale - scala 1:10.000 - estratto

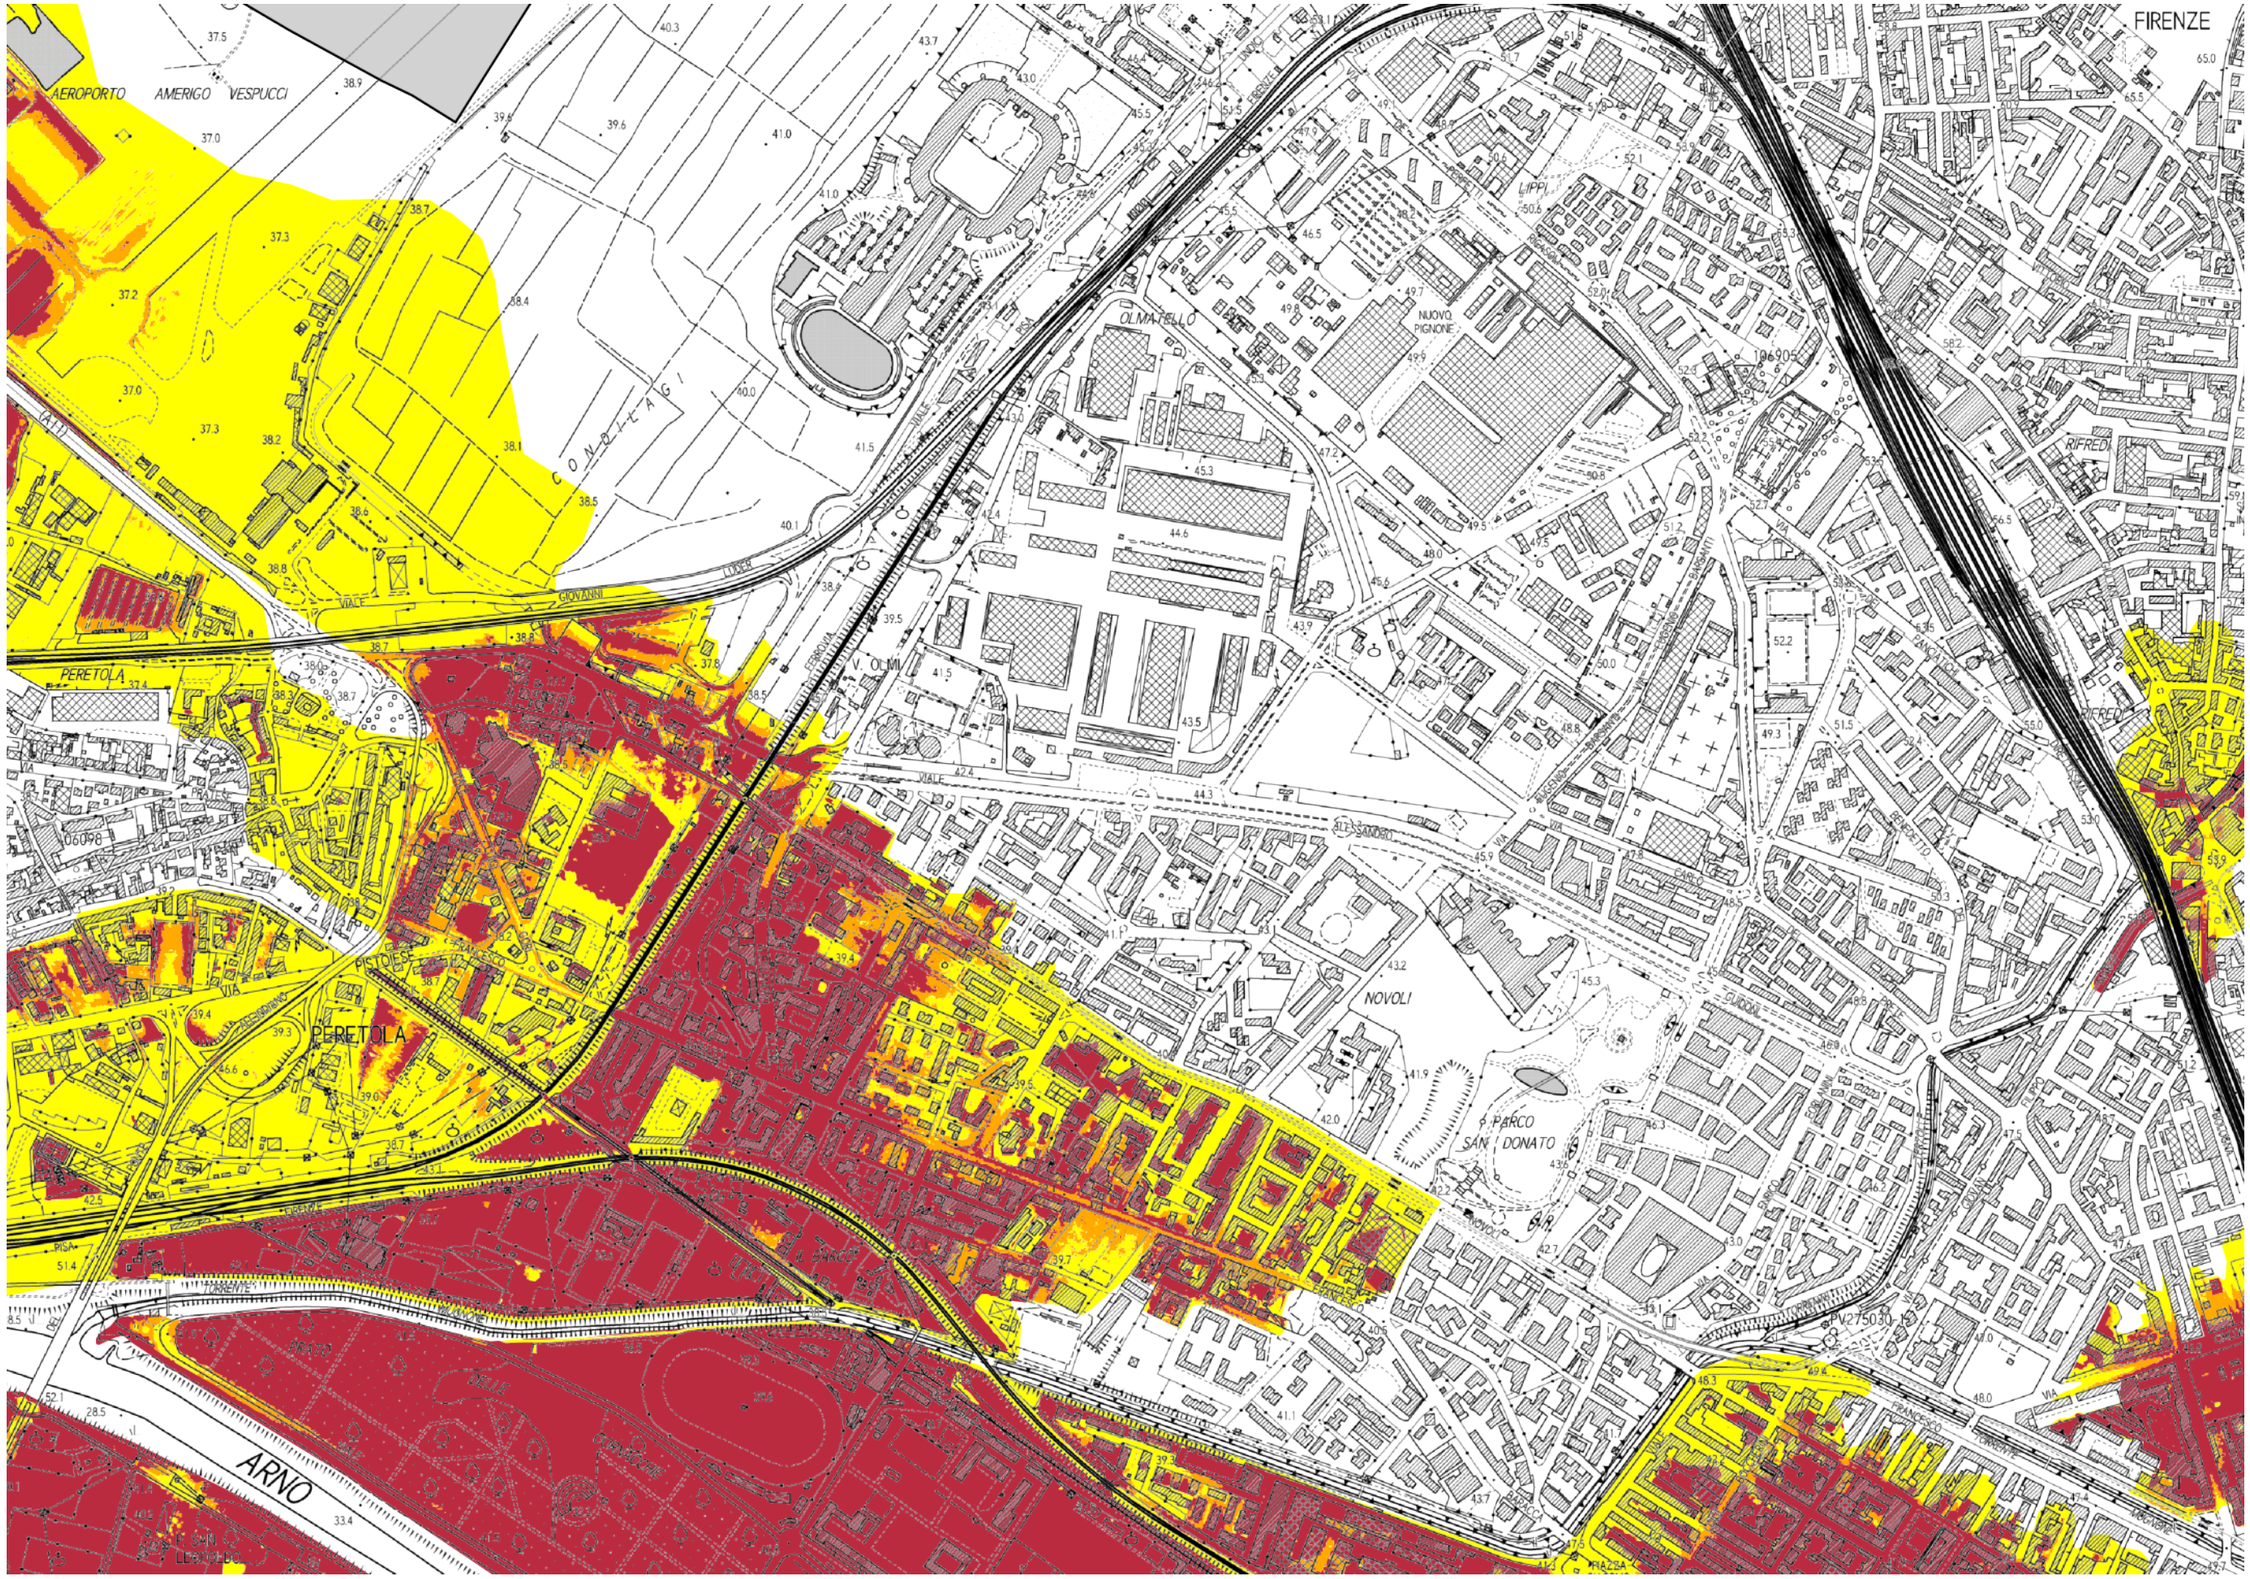

estratto alla data 20 luglio 2025

stampato il 20 luglio 2025

Comune di Firenze - Piano Strutturale

6 | pericolosita' da alluvioni - scala 1:10.000 - estratto

estratto alla data 20 luglio 2025

stampato il 20 luglio 2025

8 | sistema territoriale - scala 1:10.000 - estratto

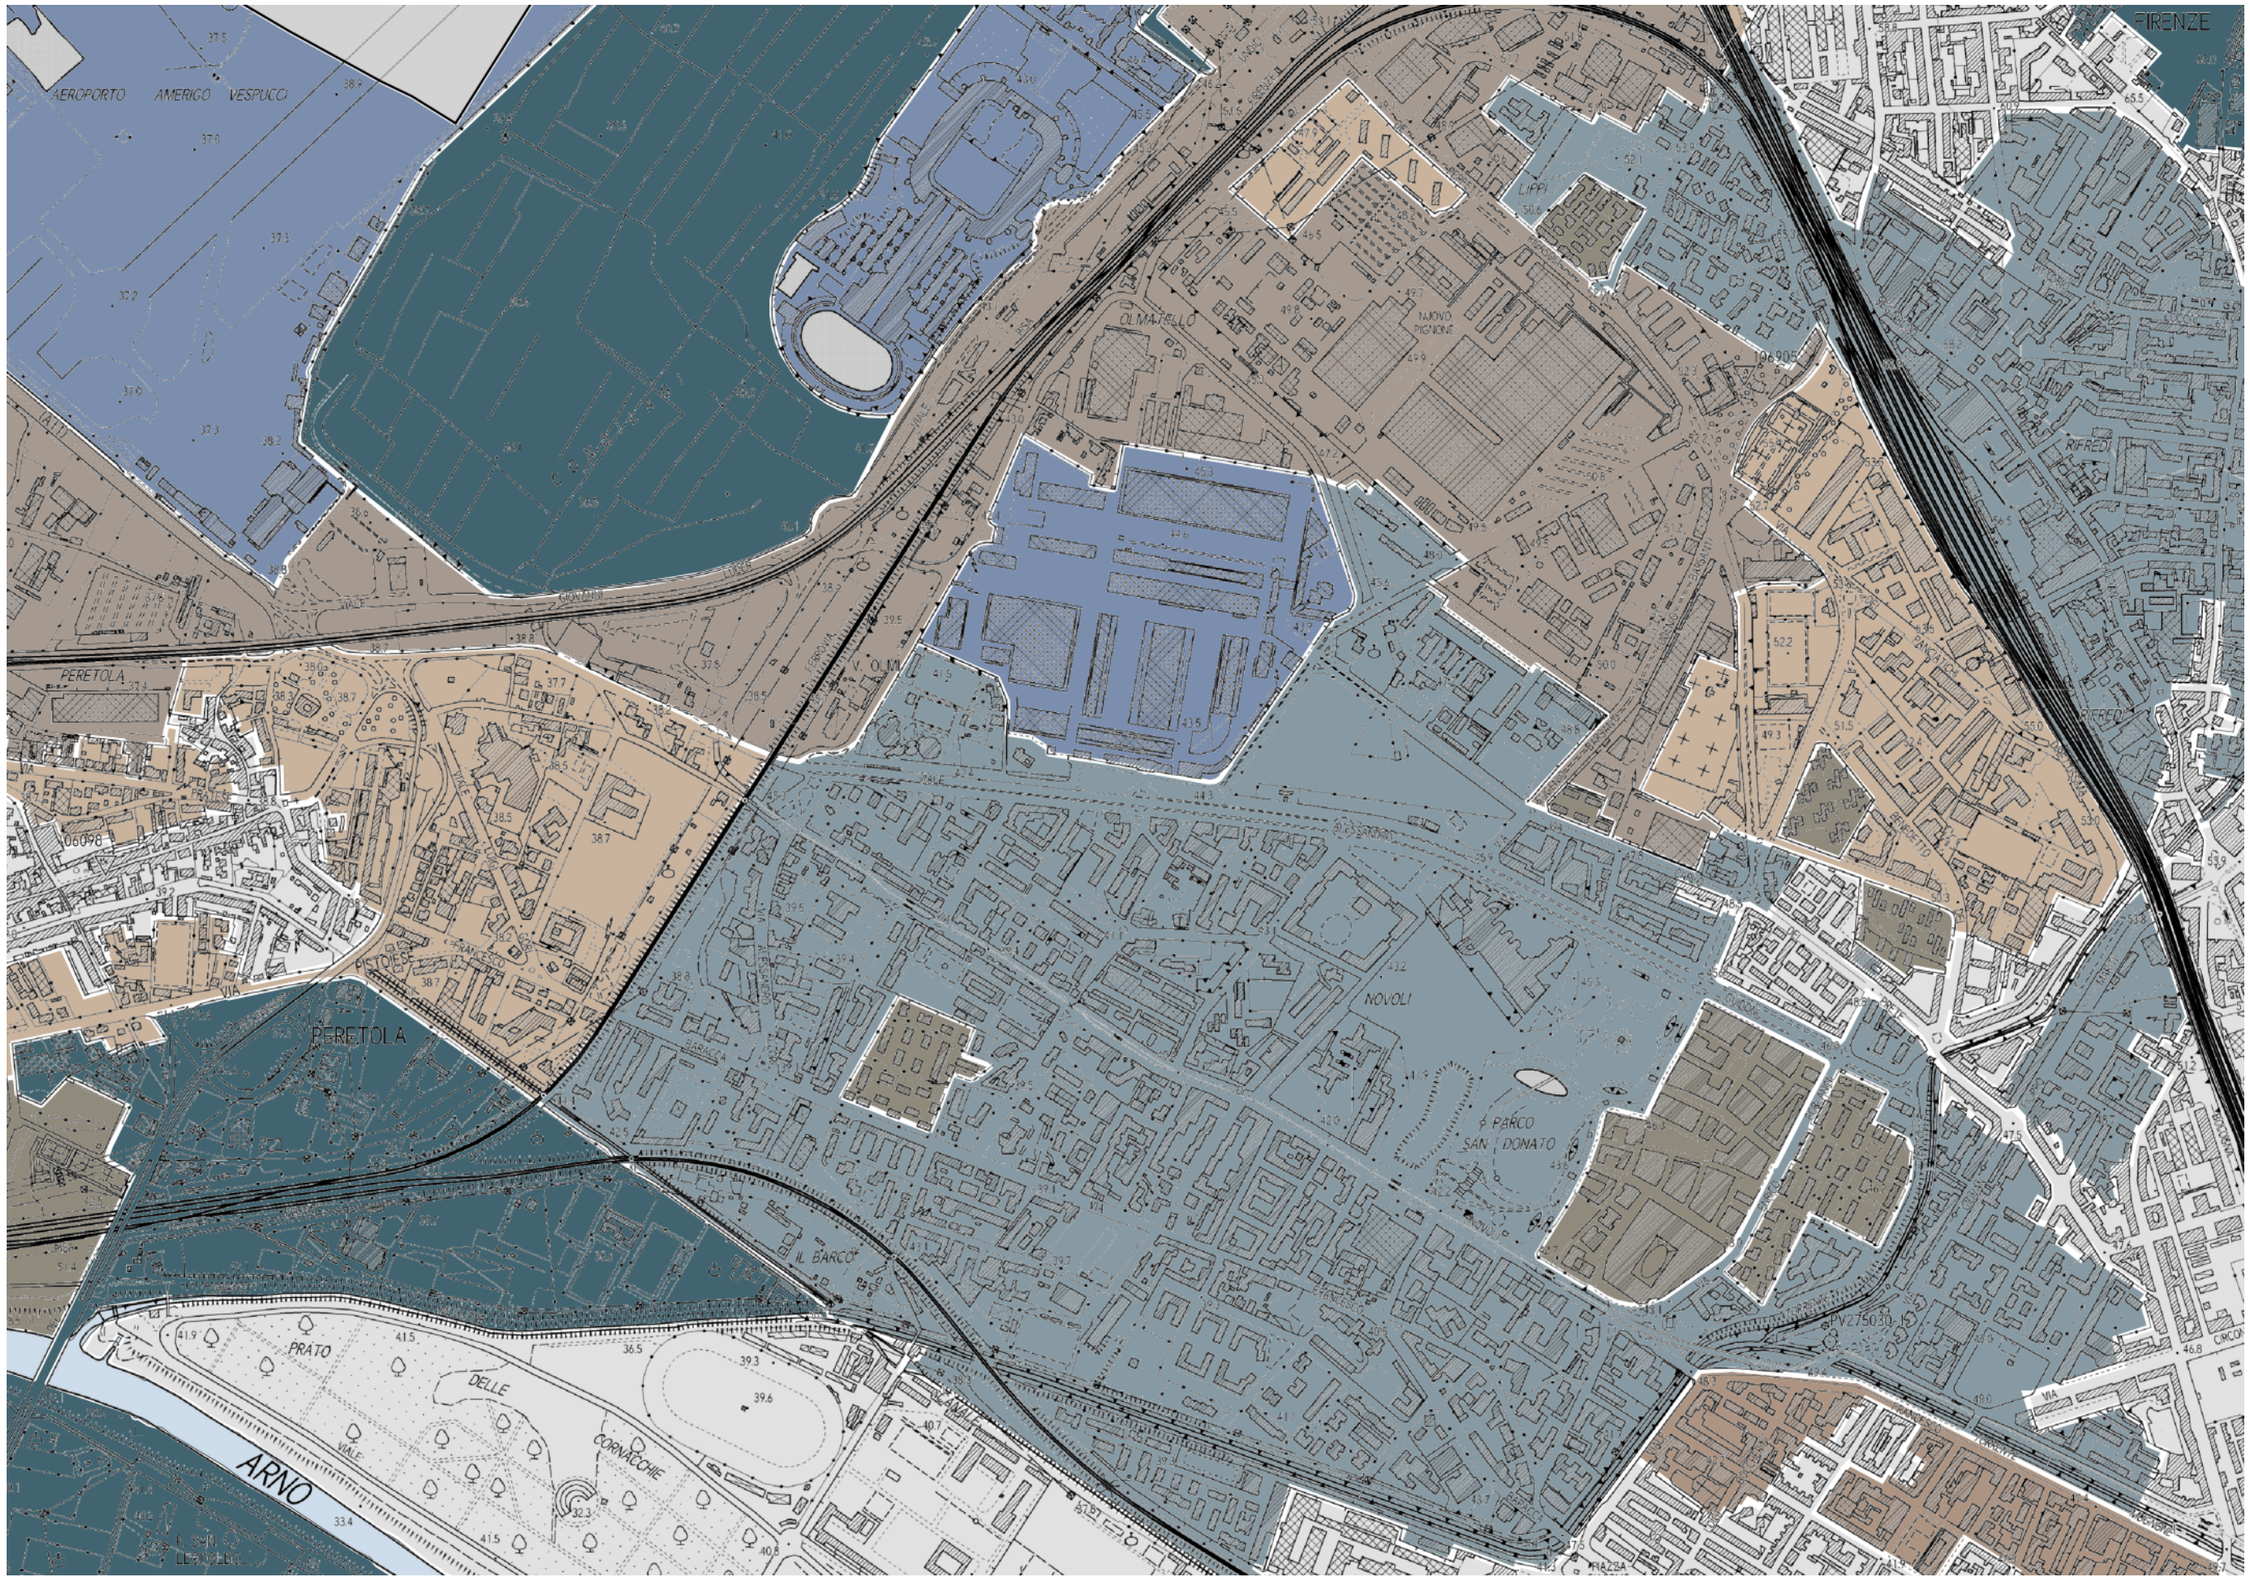

10 | mobilita' - scala 1:10.000 - estratto

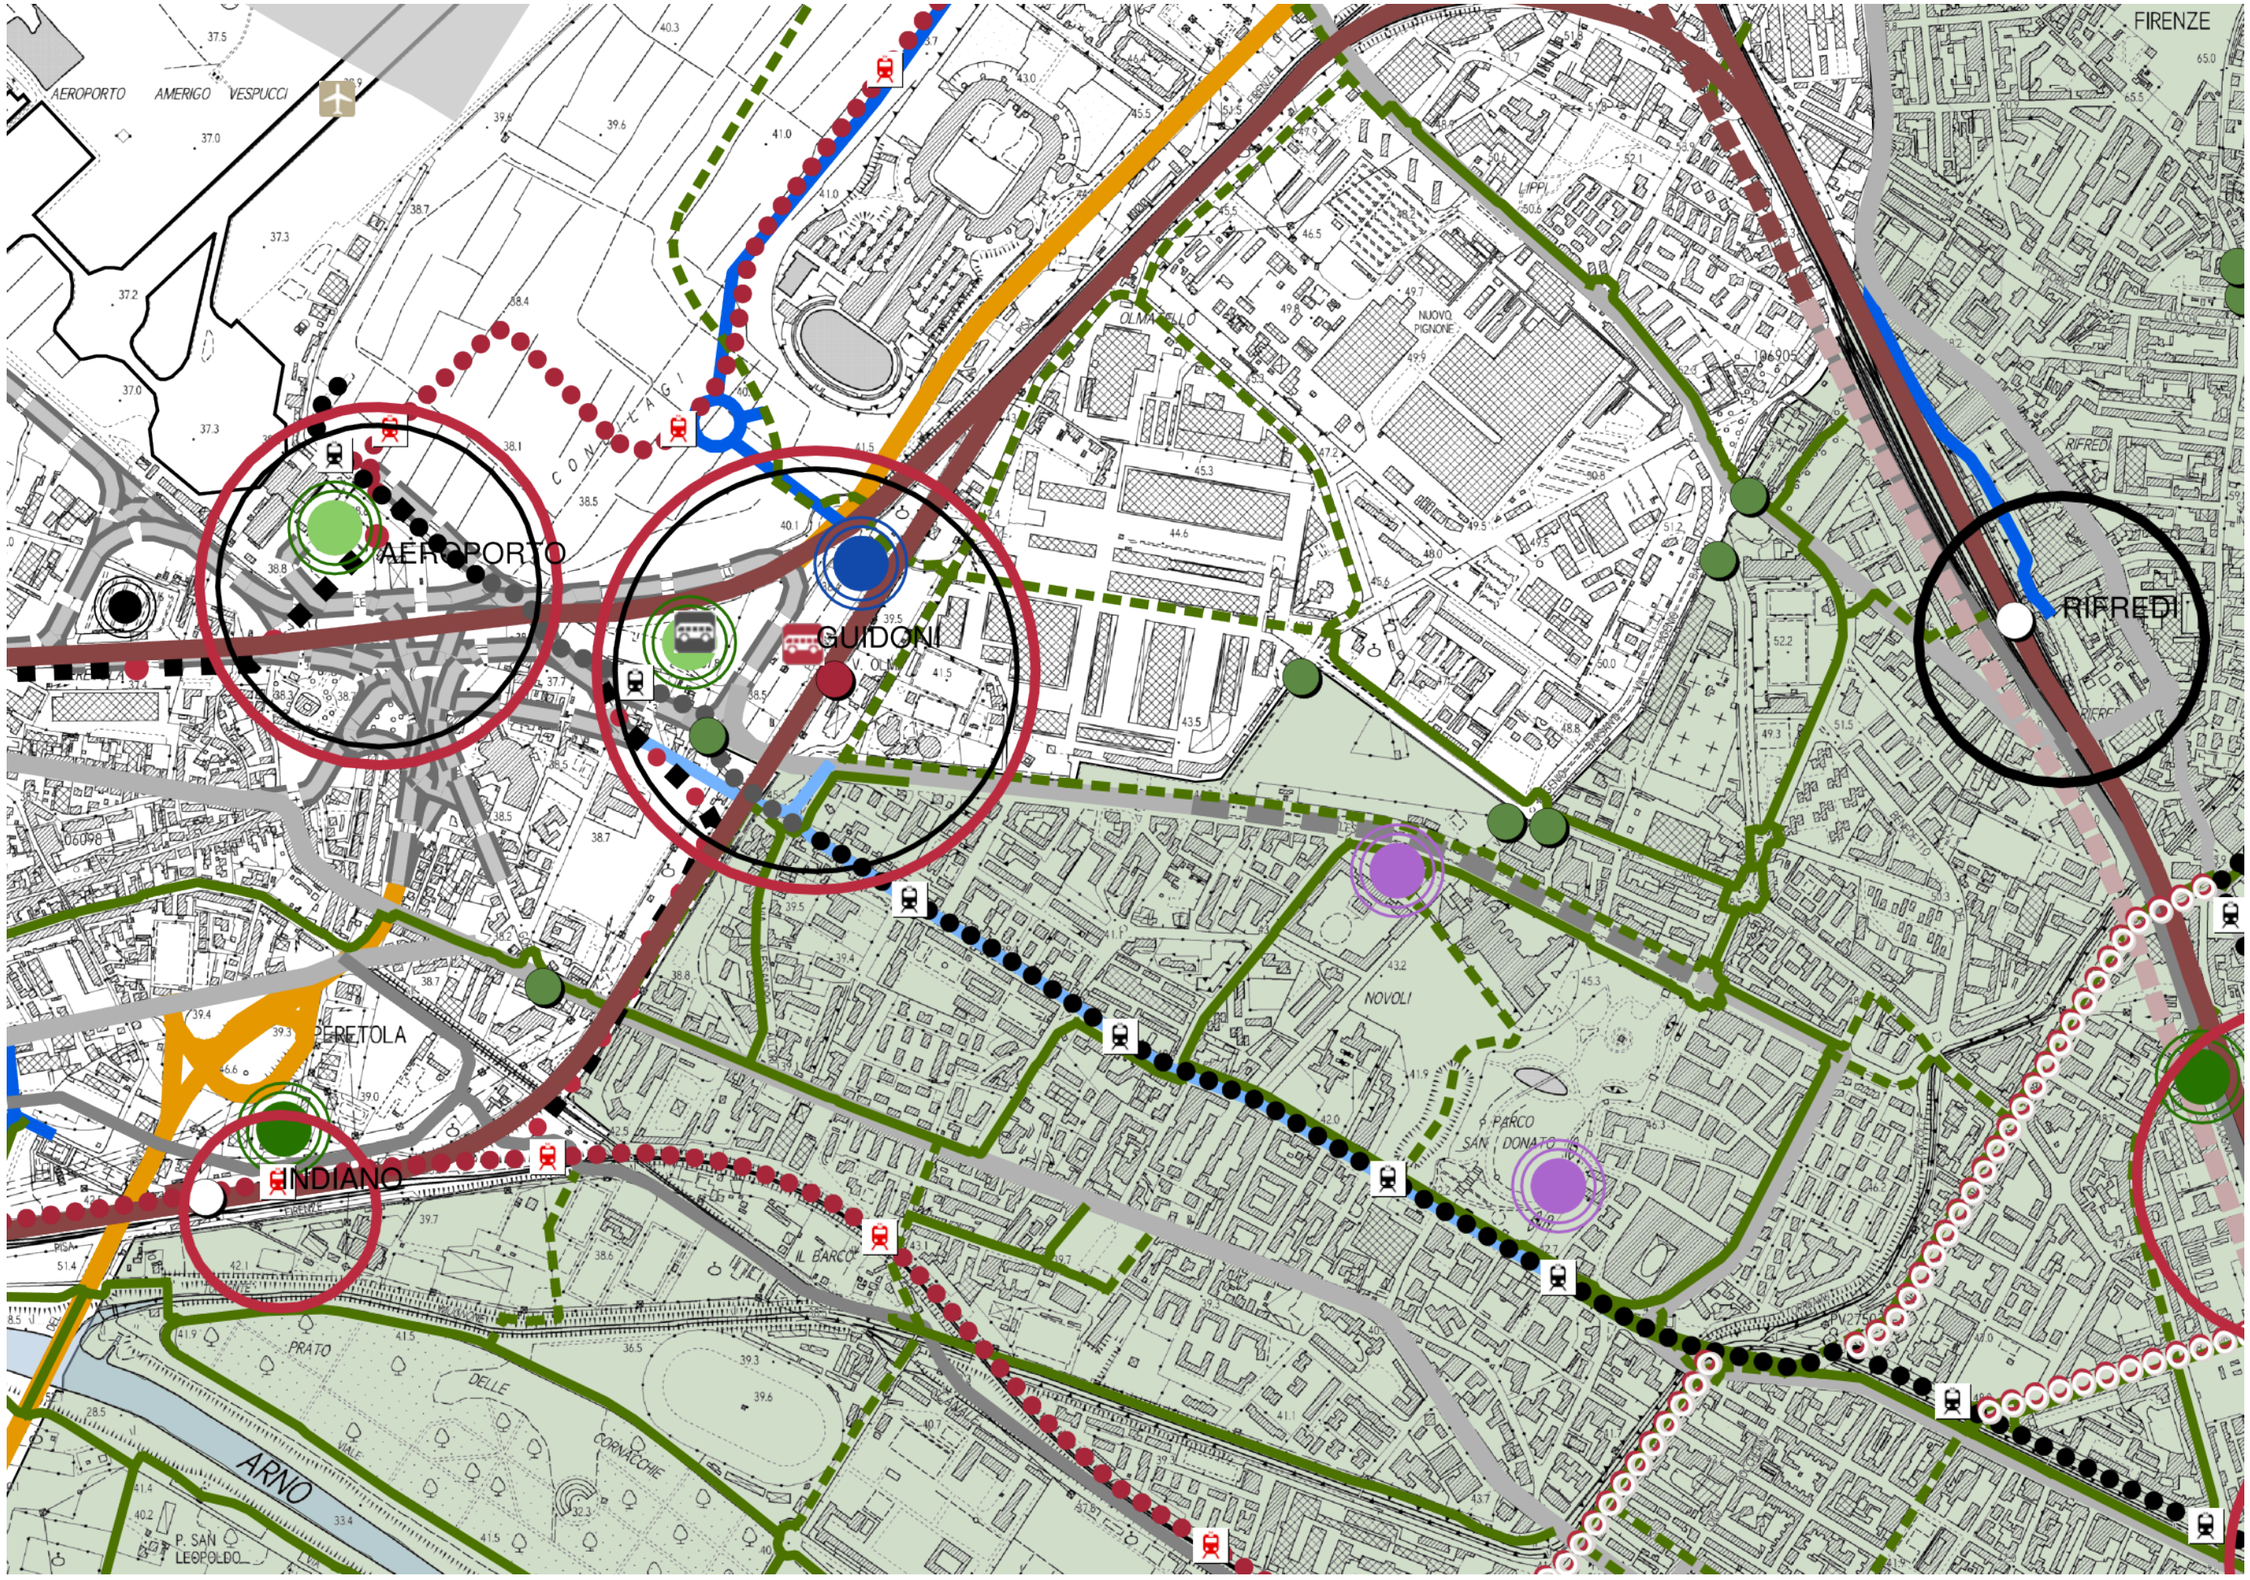

Comune di Firenze - Piano Strutturale

1 | vincoli - scala 1:10.000 - estratto

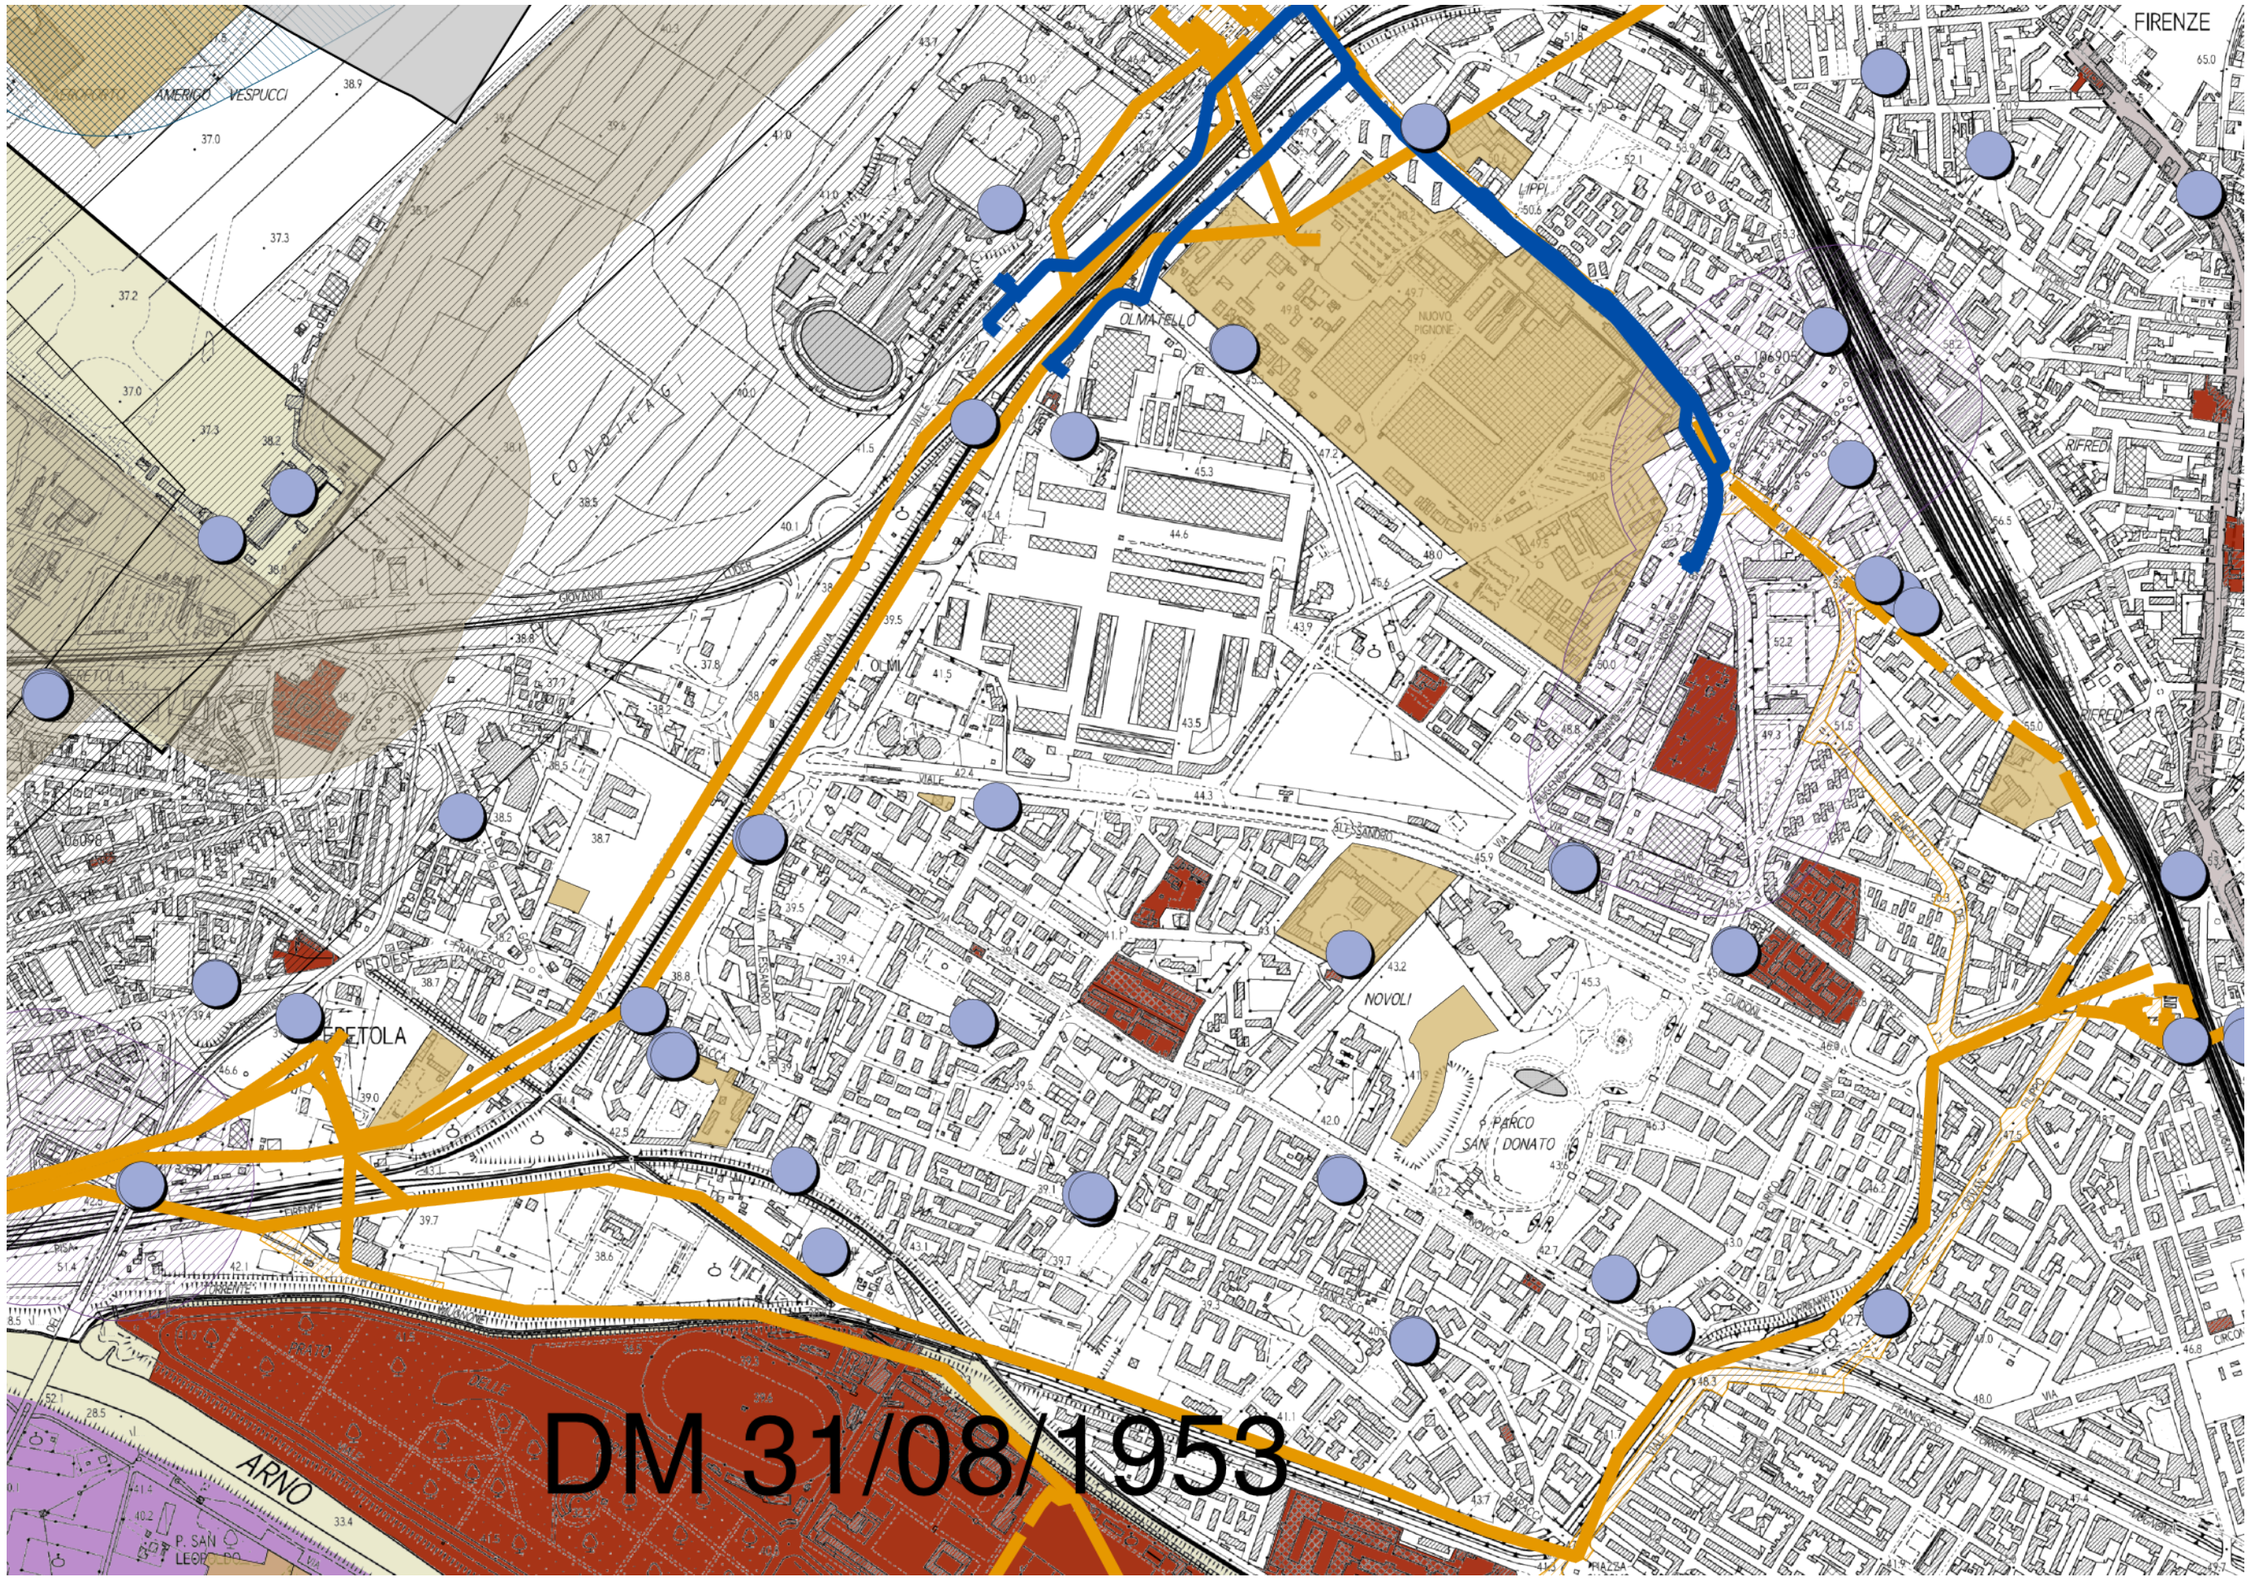

estratto alla data 20 luglio 2025

stampato il 20 luglio 2025