TEMA 1 PIANIFICATORE
Esame di Stato per Pianificatore sez. B
Sessione Estiva 2025

Lettura morfologica e classificazione dei tessuti insediativi urbani nel quartiere di Novoli – Firenze

Contesto

Il quartiere Novoli, situato nella parte nord-occidentale del Comune di Firenze, rappresenta un ambito urbano caratterizzato da una forte eterogeneità morfologica: accanto a insediamenti otto-novecenteschi si collocano interventi residenziali del secondo dopoguerra, grandi trasformazioni post-industriali e recenti polarità funzionali come il Polo universitario, la tramvia e il parco San Donato.
Il candidato è invitato a svolgere un'analisi tecnica e interpretativa dei tessuti insediativi, allo scopo di evidenziare le principali tipologie morfologiche e i caratteri strutturanti dell'organizzazione urbana, anche in funzione della pianificazione urbanistica a scala locale.

Obiettivo della prova

Analizzando gli estratti cartografici forniti (ortofoto e impianto catastale semplificato, scala 1:10.000), il candidato dovrà:
1.Identificare, delimitare e classificare i principali tessuti insediativi presenti nel quartiere:
-tessuti organici storici,
-tessuti regolari novecenteschi (a isolati, a cortina, in linea),
-ambiti a bassa densità o di frangia urbana,
-comparti di trasformazione.
2.Riconoscere gli elementi strutturanti dello sviluppo urbano:
-assi viari principali,
-nodi di interscambio e polarità funzionali,
-spazi pubblici significativi.
3.Argomentare criticamente la classificazione proposta, valutando:
-le regole storiche, morfologiche o funzionali alla base della formazione dei tessuti;
-le eventuali cesure, discontinuità o ambiti in transizione;
-i "valori urbani identitari" riscontrabili in ciascun tessuto (es. continuità spaziale, valore storico, qualità urbana, riconoscibilità insediativa).

Elaborati richiesti

1.Tavola analitica (scala a scelta):
-delimitazione e classificazione dei diversi tessuti urbani;
-individuazione di nodi, assi, polarità;
-legenda ragionata con simbologia coerente in cui argomentare descrizione delle categorie individuate e delle motivazioni;
2.Prova scritta(massimo 2 pagine):
Ipotizzando che l'Amministrazione comunale intenda inserire un piccolo centro civico all'interno del quartiere analizzato, il candidato elabori il processo di valutazione della compatibilità urbanistica, descrivendo con chiarezza:
-i passaggi tecnici e amministrativi necessari per verificarne l'ammissibilità in base agli strumenti urbanistici vigenti;
-le condizioni morfologiche e insediative che possono favorire o ostacolare l'inserimento dell'opera;

Regione Toscana

GEOscopio

Regione Toscana - SIPT: Carta tecnica regionale

Scala 1 :10.000

679.053,7

4.852.247

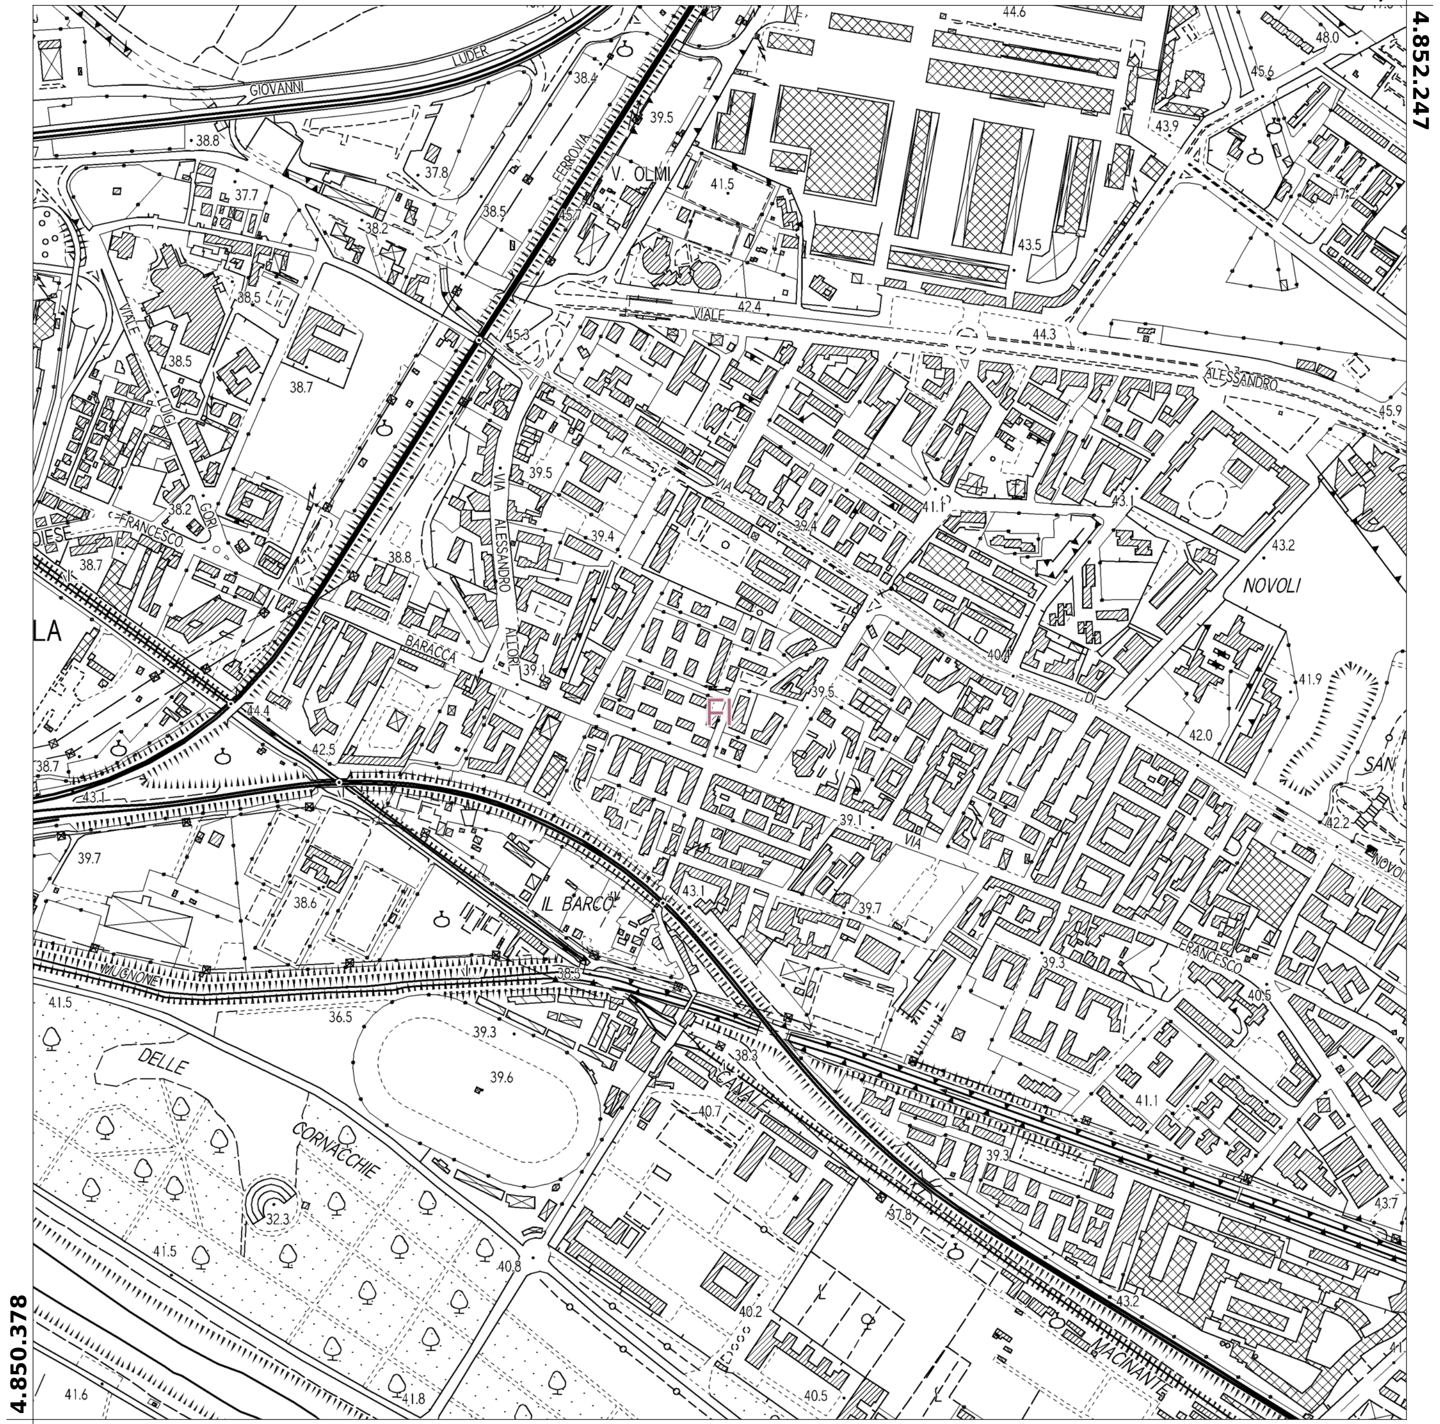

4.850.378

677.236,8

EPSG:25832

Regione Toscana

GEOscopio

Regione Toscana - SIPT: Carta tecnica regionale

Scala 1 :10.000

679.053,7

4.852.247

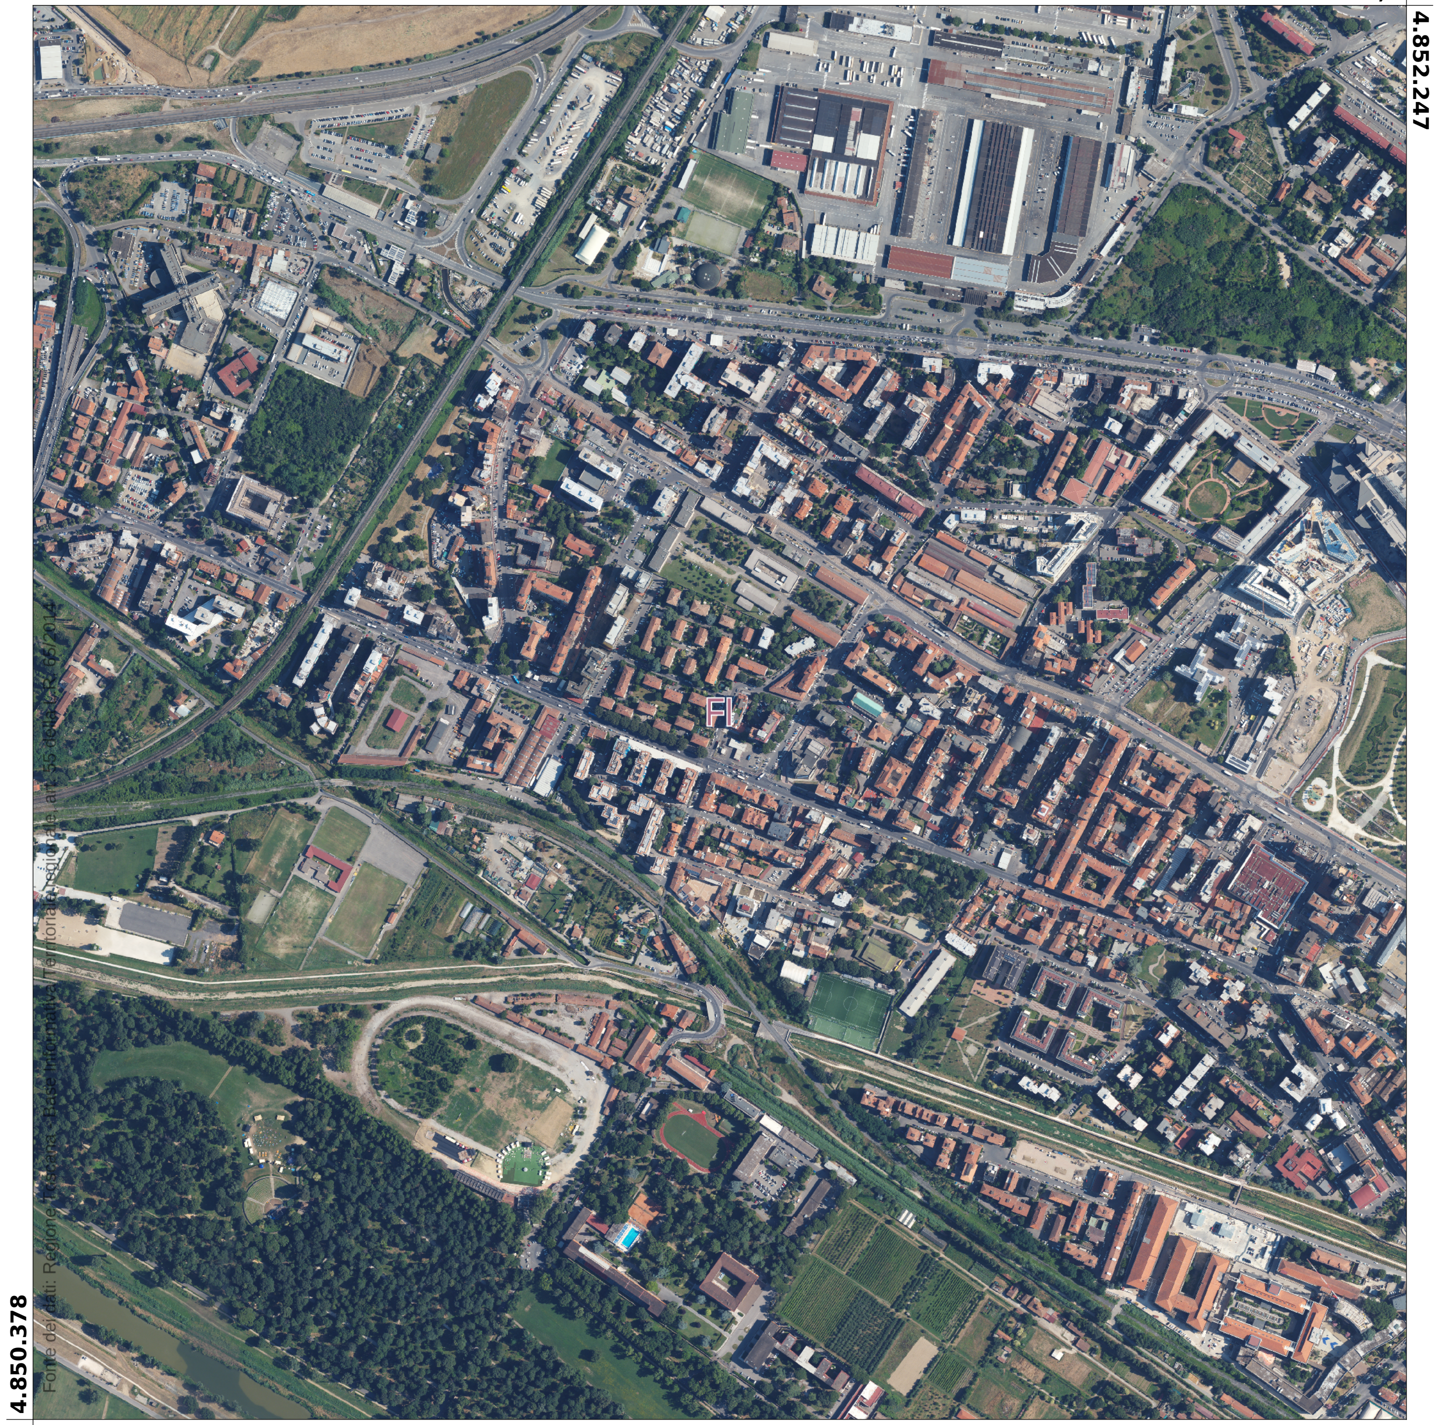

Fonte dei dati: Regione Toscana - Base Informativa Territoriale regionale, art. 55 della L.R. 65/2014

4.850.378

677.236,8

EPSG:25832