Svolgimento guidato: nuova centralità su area libera

UNIFI, II sessione 2024, traccia 1. Planivolumetrico, schema per la scheda norma e verifiche. È un esempio di metodo: una soluzione possibile, da rifare a mano con le tue scelte.

La consegna della traccia

UNIFI, II sessione 2024, prova pratica, Pianificatore Senior, traccia 1.

Traccia in PDF, pagina 1: `03_TRACCE/UNIFI_pianificatore/2024_II.pdf` · Foto aerea dell'allegato A, pagina 2: `03_TRACCE/UNIFI_pianificatore/2024_II.pdf`

In una grande area libera ai margini di un piccolo insediamento toscano, descritta dall'allegato A, l'amministrazione comunale intende promuovere una azione di rigenerazione del contesto insediativo, finalizzata alla realizzazione di una nuova centralità urbana. È previsto l'inserimento di funzioni residenziali e di servizio/commerciali, nonché la sistemazione di dotazioni a standard pubblici. L'intervento prevede inoltre la ristrutturazione della rete infrastrutturale esistente, l'inserimento di nuovi tratti stradali e la creazione di una rete di mobilità ciclopedonale, integrata al verde pubblico, in grado di collegare e mettere a sistema l'area di trasformazione col suo contesto urbano.

L'allegato B contiene una rappresentazione cartografica dell'area in scala 1:1000

Il dimensionamento dell'intervento è descritto dai dati seguenti: Superficie territoriale (ST) 40.150 mq; Superficie fondiaria (SF) 3.900 mq; Superficie edificabile (SE) 6.300 mq in totale di cui: SE residenziale 1.260 mq; SE direzionale 4.290 mq; SE 500 mq commerciale di vicinato. Si prevede inoltre la sistemazione di edilizia residenziale sociale (ERS) per una SE di 250 mq. Altezze ammesse: 2 piani fuori terra per la funzione residenziale; fino a 3 piani fuori terra per la funzione direzionale.

L'intervento dovrà prevedere la sistemazione di dotazioni pubbliche relative a: Verde pubblico; Parcheggi pubblici; Viabilità ciclo pedonale; Piazza pedonale.

Il candidato/la candidata sviluppi i parametri quantitativi previsti attraverso un planivolumetrico in scala almeno 1/1000 avendo cura di rappresentare:

- l'organizzazione della viabilità interna all'area di intervento, sia carrabile che ciclo-pedonale
- la localizzazione della piazza pubblica
- la localizzazione e il dimensionamento dei parcheggi pubblici; la localizzazione e il dimensionamento dei parcheggi pertinenziali privati
- la localizzazione delle edificazioni previste e i caratteri tipologici utilizzati
- la localizzazione e i caratteri della vegetazione da utilizzare per la valorizzazione delle aree a verde pubblico

Sintetizzi i caratteri della prefigurazione progettuale in uno schema adatto a corredare la scheda norma della trasformazione prevista negli apparati uno strumento di pianificazione operativa.

Illustri attraverso testi e tabelle la verifica dei dimensionamenti previsti, inclusi gli standard a parcheggio e a verde pubblico, nonché dei parcheggi pertinenziali, facendo puntuale riferimento alla normativa vigente

Trascrizione dalla scansione: in caso di dubbio fa fede il PDF.

> **Prima di leggere.** Fermati dopo la sezione 2 e fai da te i conti, poi uno schizzo con le macchie delle funzioni. Il confronto vale più della soluzione.

1. Cosa chiede davvero la traccia

Il dato che decide tutto è la **SF di 3.900 mq su una ST di 40.150**: appena il 9,7%. Più del 90% dell'area resta pubblica. Non stai disegnando un quartiere con un po' di verde: stai disegnando un parco, con un piccolo centro compatto dentro.

Il secondo dato è la densità. L'indice territoriale è basso, 0,16 mq/mq. Quello fondiario è alto, 1,62 mq/mq. Su quei 3.900 mq non ci stanno insieme edifici, parcheggi privati e il 25% di suolo permeabile. Devi accorgertene subito e risolverlo con l'interrato.

Il terzo è un nodo di norma. La traccia parla di «rigenerazione», ma l'area è libera. Il capo sulla rigenerazione (LR 65, artt. 122-125) riguarda aree con degrado e patrimonio edilizio o attrezzature dismesse, dentro il territorio urbanizzato (art. 122 c. 2; art. 123). Qui lo strumento è il **piano attuativo** previsto dal piano operativo (art. 95 c. 3 lett. a; artt. 107 e 109). E c'è una condizione: la residenza nuova è ammessa solo nel territorio urbanizzato (art. 4 c. 2). Se l'area fosse fuori, il programma non starebbe in piedi: lo dichiari in testa alla relazione.

La traccia chiede	Dove lo metti	Errore da evitare
Viabilità interna, carrabile e ciclopedonale	Tavola e due sezioni	Dimenticare il varco stradale a est, già dato dal perimetro
Piazza pubblica	Tavola, con misure	Una piazza attraversata dalle auto
Parcheggi pubblici e pertinenziali, posizione e misura	Tavola e tabelle	Sommare tutto sui 3.900 mq senza accorgersi che non ci sta
Edifici e caratteri tipologici	Tavola e tabella tipologie	Superare i piani ammessi; edifici senza piani scritti
Vegetazione del verde	Tavola e testo	Tagliare i boschi per «fare» il parco
Schema per la scheda norma	Schema separato e tabella	Ridurre la tavola senza distinguere prescrittivo e indicativo
Verifica con norme puntuali	Tabelle in relazione	Citare leggi senza il calcolo

2. Il metodo e i tempi

N.	Passaggio	Tempo	Domanda	Prodotto
1	Scomponi	15 min	Quali elaborati e dati?	Lista di controllo
2	**Conti**	40 min	Standard, parcheggi, copertura?	Tabelle complete
3	Leggi il luogo	40 min	Strade, varchi, alberi, fronti?	Schizzo su lucido
4	Macchie	40 min	Dove sta il centro, e perché?	Due alternative, una scelta
5	Bilancio	20 min	Le superfici tornano?	Tabella che somma alla ST
6	Planivolumetrico	140 min	Strade, lotti, edifici, parcheggi, alberi	Tavola a penna 1:1000
7	Sezioni	20 min	Si capisce la strada?	Due sezioni
8	Schema per la scheda norma	30 min	Cosa è obbligo, cosa è indicazione?	Schema e tabella
9	Relazione	55 min	Perché queste scelte?	Testo e tabelle
10	Rilettura	20 min	Ho risposto a tutto?	Lista spuntata

Totale 7 ore, con un'ora di margine sulle 8 ore della prova.

3. I conti

Controllo dei dati

1.260 + 4.290 + 500 = 6.050. Con i 250 di ERS fa **6.300**: l'ERS è dentro il totale, non in più. Dichiaralo, perché la frase della traccia («inoltre») si presta all'equivoco.

Standard

Abitanti: 1.510 ÷ 30 = 50,3, arrotondato a **51**. Il 30 viene dai 25 + 5 mq per abitante del DM 1444, art. 3. Se il Comune ha un altro indice, usa quello (DPGR 39/R, art. 2).

Funzione	Calcolo	mq	Di cui
Residenza ed ERS (DM 1444, art. 3)	51 × 18	**918**	Istruzione 229,5 · interesse comune 102 · verde 459 · parcheggi 127,5
Direzionale e commerciale (art. 5 n. 2)	4.790 × 0,80	**3.832**	Almeno 1.916 a parcheggio
Totale minimo		**4.750**	Parcheggi pubblici minimi: **2.043,5** mq, 82 posti

Tre note. Non applico la riduzione dell'art. 5 n. 2 per le zone A e B: su un'area libera ai margini sarebbe difficile sostenerla. L'alloggio sociale è uno standard aggiuntivo (LR 65, art. 63 c. 3): non sostituisce quelli del DM. La traccia non elenca scuole né attrezzature, ma l'art. 3 ripartisce i 18 mq «di norma»: riservo 340 mq e lo dico. Se vuoi usare diversamente quella quota, devi motivarlo nel piano.

Parcheggi pertinenziali

Un metro quadrato ogni 10 mc (L. 1150/42, art. 41-sexies; DPGR 39/R, art. 37). Il volume è virtuale: SE per 3,00 m o 3,50 m a seconda della funzione (DPGR 39/R, art. 24 c. 3). Le aree comprendono gli spazi di manovra (art. 37 c. 1).

Funzione	SE × altezza	Volume (mc)	Parcheggio (mq)	Posti a 25 mq
Residenza ed ERS	1.510 × 3,00	4.530	453	18
Direzionale	4.290 × 3,00	12.870	1.287	51
Commerciale	500 × 3,50	1.750	175	7
Totale		**19.150**	**1.915**	**77**

Calcolo per funzione, cioè per unità immobiliare (art. 24 c. 2 lett. b). Con il volume dell'intero edificio e l'altezza della funzione prevalente (art. 24 c. 4) il commercio peserebbe 25 mq in meno: tengo il valore più alto.

Sosta di relazione

La superficie di vendita non è in traccia. Ipotizzo **300 mq** su 500 di SE, divisi in negozi di vicinato. Servono 300 mq, 1 mq per mq di vendita (DPGR 23/R, art. 9 c. 1), su area privata o con uso pubblico garantito negli orari di apertura (art. 8 c. 3). Il 10% è per il personale (art. 8 c. 4).

Quanto ci sta sui 3.900 mq

Questa è la verifica che distingue la prova. Il commercio al piano terra dell'edificio direzionale fa risparmiare suolo.

Voce	Calcolo	mq
Direzionale e commercio, 3 piani	4.790 ÷ 3	1.597
Residenza ed ERS, 2 piani	1.510 ÷ 2	755

Voce	Calcolo	mq
Superficie coperta	Indice di copertura 60% (DPGR 39/R, art. 16)	**2.352**
Resta libero	3.900 – SC	1.548
Permeabile minimo, 25% della SF	DPGR 39/R, art. 26 c. 2	975
Sosta privata da collocare	1.915 + 300	**2.215**

La sosta privata (2.215 mq) supera tutto il suolo libero (1.548 mq). A raso non ci sta. **Soluzione: autorimesse interrate.** Attenzione: un solaio interrato non è superficie permeabile (DPGR 39/R, art. 25 c. 1). Quindi l'interrato deve restare quasi sotto gli edifici, come mostra la tabella. Entro le dotazioni minime e con altezza utile fino a 2,40 m, nel territorio urbanizzato le autorimesse non fanno SE (art. 10 c. 2 lett. b.8).

Lotto	SF	SC	Interrato	Libero da solai	Minimo 25%	Esito
Direzionale e commercio	2.500	1.597	1.762 (stanziale 1.462 + relazione 300)	738	625	Sì
Residenza ed ERS	1.400	755	Sotto la sagoma: 453 a parcheggio, il resto cantine e impianti	645	350	Sì

Bilancio delle superfici

Le aree derivano dal disegno, calcolate nel codice. La scala nasce dalla ST: in aula la leggi dall'allegato B.

Voce	mq	% di ST
Strada esistente, sezione attuale 9 m	2.305	5,7%
Nuova strada di collegamento	1.875	4,7%
Strada di servizio	700	1,7%
Percorsi ciclopedonali nel verde	1.351	3,4%
Lotto direzionale e commerciale (SF)	2.500	6,2%
Lotto residenziale ed ERS (SF)	1.400	3,5%
Piazza pedonale	2.400	6,0%
Parcheggi pubblici	2.100	5,2%
Area riservata ad attrezzature	340	0,8%
Verde pubblico	25.179	62,7%
Totale, pari alla ST	**40.150**	**100%**

Verifica

Voce	Minimo	Progetto	Esito
Parcheggi pubblici (DM 1444, artt. 3 e 5; DPGR 39/R, art. 39)	2.043,5	2.100, 84 posti	Sì
Verde pubblico per la residenza (art. 3 lett. c)	459	25.179, escluse le fasce lungo strada dal conteggio minimo	Sì, ampiamente
Istruzione e interesse comune (art. 3 lett. a, b)	331,5	340	Sì, come area riservata
Quota restante di direzionale e commerciale (art. 5 n. 2)	1.916	Piazza, 2.400	Sì: scelta mia, contare la piazza va motivato

Voce	Minimo	Progetto	Esito
Pertinenziali (art. 41-sexies)	1.915	Interrati nei due lotti	Sì
Relazione (DPGR 23/R, art. 9)	300	Interrato del lotto direzionale, con uso pubblico	Sì, sulla SV ipotizzata
Permeabilità, 25% della SF	625 · 350	738 · 645	Sì
Piani (traccia)	2 residenza · 3 direzionale	2 · 3	Sì
SE (traccia)	6.300	6.300	Sì
SF (traccia)	3.900	3.900	Sì

Confronto con il Kit

Ho ricalcolato nel codice l'esempio del Kit.

Voce	Calcolo del Kit	Kit	Ricalcolo	Esito
SE residenziale totale	1.260 + 250	1.510	1.510	Uguale
Abitanti	1.510 ÷ 30 = 50,3 → 51	51	51	Uguale
Standard residenziali	51 × 18	918	918	Uguale
Standard non residenziali	4.790 × 0,80	3.832	3.832	Uguale
Di cui parcheggi	3.832 ÷ 2	1.916	1.916	Uguale
Totale standard	918 + 3.832	4.750	4.750	Uguale
Parcheggi pubblici minimi	127,5 + 1.916	2.043,5	2.043,5	Uguale
Pertinenziali	4.530 + 12.870 + 1.750 = 19.150 mc	1.915	1.915	Uguale
Copertura	2.685 ÷ 3.900	0,69	0,69 con le ipotesi del Kit; **0,60** con la mia	Differenza di ipotesi, non errore

Il Kit somma 500 mq di commercio separati dal direzionale. Io li metto al piano terra dello stesso edificio. Sono ipotesi diverse e la traccia non impone nessuna delle due.

4. La lettura dell'area

Tavola: il contesto

La base è la foto dell'allegato A. Nel nostro PDF manca l'allegato B: in aula lavora su quello.



1 Strada principale a nord
Corre tra le case con un attraversamento pedonale. La strada interna ci si innesta.

2 Strada interna esistente
Rettifilo di circa 256 m, largo circa 9 m. Taglia l'area in due parti molto diverse: è la rete da ristrutturare.

3 Nodo sud
Incrocio con la strada est-ovest e strisce pedonali verso gli isolati a sud.

4 **Il dito a est**
Il perimetro si allunga in una lingua larga circa 7 m fino alla via di quartiere. Non è un caso: è il varco per il nuovo tratto stradale.

5 **Fascia vegetata**
Linea di arbusti e alberi parallela alla strada, a est. Sembra un fosso: la foto non basta, va verificato.

6 **Macchia alberata est**
Massa di alberi nella metà sud del lotto est. Si conserva.

7 **Macchia alberata ovest**
Copre quasi tutto il lotto ovest, verso la ferrovia.

8 **Prato centrale**
Prato con alberi isolati: è il suolo libero meno costoso da trasformare.

9 **Radura a nord-ovest**
Terreno chiaro già aperto, a filo strada: adatto alla sosta.

10 **Ferrovia**
Lambisce l'angolo sud-ovest. Fascia di rispetto da riscontrare.

11 **Fronte est e nord**
Villette e palazzine basse, con retri sul confine.

12 **Isolati a sud**
Grandi edifici in linea: è il bacino più denso, senza un centro proprio.

Il perimetro ha la stessa giacitura delle strade e dei confini: il lotto est è quasi un rettangolo di 100 × 210 m. Il disegno segue quella griglia.

5. Le scelte, in ordine

1. **Prima la rete.** La strada interna diventa un viale con ciclabile. Il nuovo tratto parte dal varco a est e arriva alla strada interna: lega il quartiere est, oggi chiuso, al resto.
2. **Il centro dove le due strade si incrociano.** È il punto più raggiungibile di tutta l'area, e il prato costa meno degli alberi.
3. **La piazza a nord della nuova strada.** Così gli edifici le stanno a nord, guarda a sud e prende sole (nord in alto, assunto: l'allegato non lo indica). Le auto la lambiscono, non la attraversano.
4. **Negozi sulla piazza, uffici sopra.** L'edificio più alto sta verso la strada interna. Le case stanno a est, con altezza simile a quella delle villette vicine.
5. **Le auto sotto.** Una strada di servizio a nord porta alle rampe. La piazza resta libera.
6. **I boschi restano.** Sono il parco. Non servono nuovi impianti massicci, ma percorsi e radure.

Alternativa scartata: centro vicino al nodo sud. Sarebbe più vicino agli isolati densi, ma taglierebbe i boschi e lascerebbe isolato il quartiere nord-est.

6. Gli elaborati

Tavola: planivolumetrico



A **Direzionale e commercio**
Edificio a corte aperta di 3 piani, SC 1.597 mq. Piano terra: negozi (SE 500) e uffici. Sopra: uffici. Lotto di 2.500 mq.

B **Residenza ed ERS**
Corpo a L di 2 piani, SC 755 mq, circa 18 alloggi (ipotesi 85 mq). Testata sud con l'ERS. Lotto di 1.400 mq.

C **Piazza pedonale**
2.400 mq, 60 × 40 m. Portico a nord, alberi a est, strada calma a sud.

P **Parcheggi pubblici**
1.320 mq a sud della nuova strada, 780 mq nella radura a nord-ovest: 84 posti circa.

S **Area per attrezzature**
340 mq riservati a istruzione e interesse comune. Nessuna SE prevista: vedi sezione 3.

V **Verde pubblico**
25.179 mq: boschi conservati e prati. Include la fascia vegetata F.


F **Fascia vegetata**
Si conserva. È attraversata solo dalle due strade.

Linea verde tratteggiata: percorsi ciclopedonali. Frecce nere: rampe delle autorimesse. Rettangolo tratteggiato nella corte: parte dell'interrato oltre la sagoma, 165 mq. Macchie verdi: boschi, disegnati in modo schematico. Disegno a scala di foto: a 1:1000 lo riporti sull'allegato B.


Viabilità

Tratto	Sezione	Note
Strada esistente	9 m attuali, da riordinare	Carreggiata 6,5 e marciapiede 2,5 nella sede attuale; aiuola e ciclopedonale a est, nel verde. Il rettifilo invita a correre: attraversamenti rialzati a nord, al centro e a sud.
Nuovo collegamento	14 m nel lotto, 7 m nel varco	Lungo circa 149 m. Zona 30. Nel varco la ciclabile torna su strada: carreggiata 5,5 e marciapiede 1,5.
Strada di servizio	6 m	Fondo cieco, serve le rampe e il passo carrabile. Va verificato lo spazio di manovra in testa.
Percorsi	3 m, circa 450 m in totale	Dal nodo nord al nodo sud lungo il viale; dal centro al nodo sud nel bosco; sentiero esistente verso ovest; passaggio tra i lotti verso la piazza.

Sezione della strada esistente

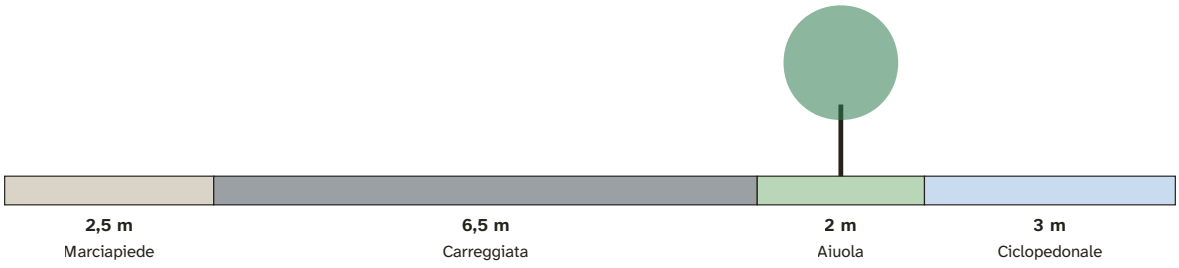

Sezione del nuovo collegamento

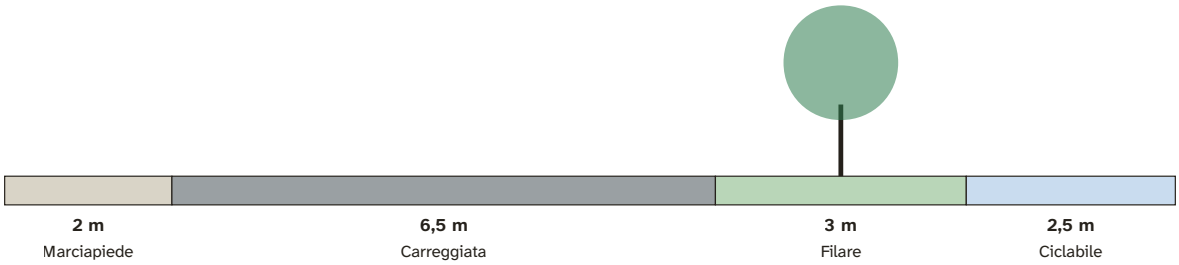

Larghezze di progetto: controlla la categoria della strada e il DM 5/11/2001 sul caso.

Caratteri tipologici

Edificio	Tipo	Piani	Perché
Direzionale e commercio	Corte aperta a nord, manica 16 m, portico sulla piazza	3	Fronte continuo a sud. La corte, su solaio solo in parte, tiene suolo permeabile.
Residenza ed ERS	Corpo in linea a L, manica 12,5 m, giardino a sud-est	2	Scala delle villette vicine. Ogni alloggio ha doppio affaccio.
ERS	Testata sud del corpo, circa 3 alloggi sulla SE di 250 mq	2	Stessa architettura del resto, sulla piazza: niente separazione sociale.


Distanze: lo spazio tra i due lotti è 12 m, per rispettare 10 m e, se la zona è C, anche l'altezza del più alto (DM 1444, art. 9). Ipotizzo meno di 12 m per 3 piani: verifica l'altezza reale.

Vegetazione

Dove	Carattere	Perché
Boschi est e ovest	Si conservano. Diradamento e sottobosco solo dopo un rilievo	Dalla foto non riconosco le specie né lo stato: possono esserci specie invasive
Fascia vegetata	Si conserva e si infittisce con arbusti e specie di ripa, se è un fosso	Corridoio ecologico nord-sud
Viale e nuovo collegamento	Filare continuo di alberi grandi e caducifogli su aiuola drenante	Ombra d'estate, sole d'inverno, disegno della strada
Piazza	Pochi alberi a chioma ampia sul lato est, resto libero	Lascia spazio a mercati ed eventi
Parcheggi	Filari ai margini, stalli in pavimentazione drenante	Ombra e permeabilità (DPGR 39/R, art. 25 c. 2)
Confine nord	Siepe e alberi di media grandezza	Filtro verso i retri delle case

Le specie vanno scelte dopo aver visto il luogo. Se devi citarne in aula, proponi specie autoctone e dichiarale come proposta.

Schema per la scheda norma

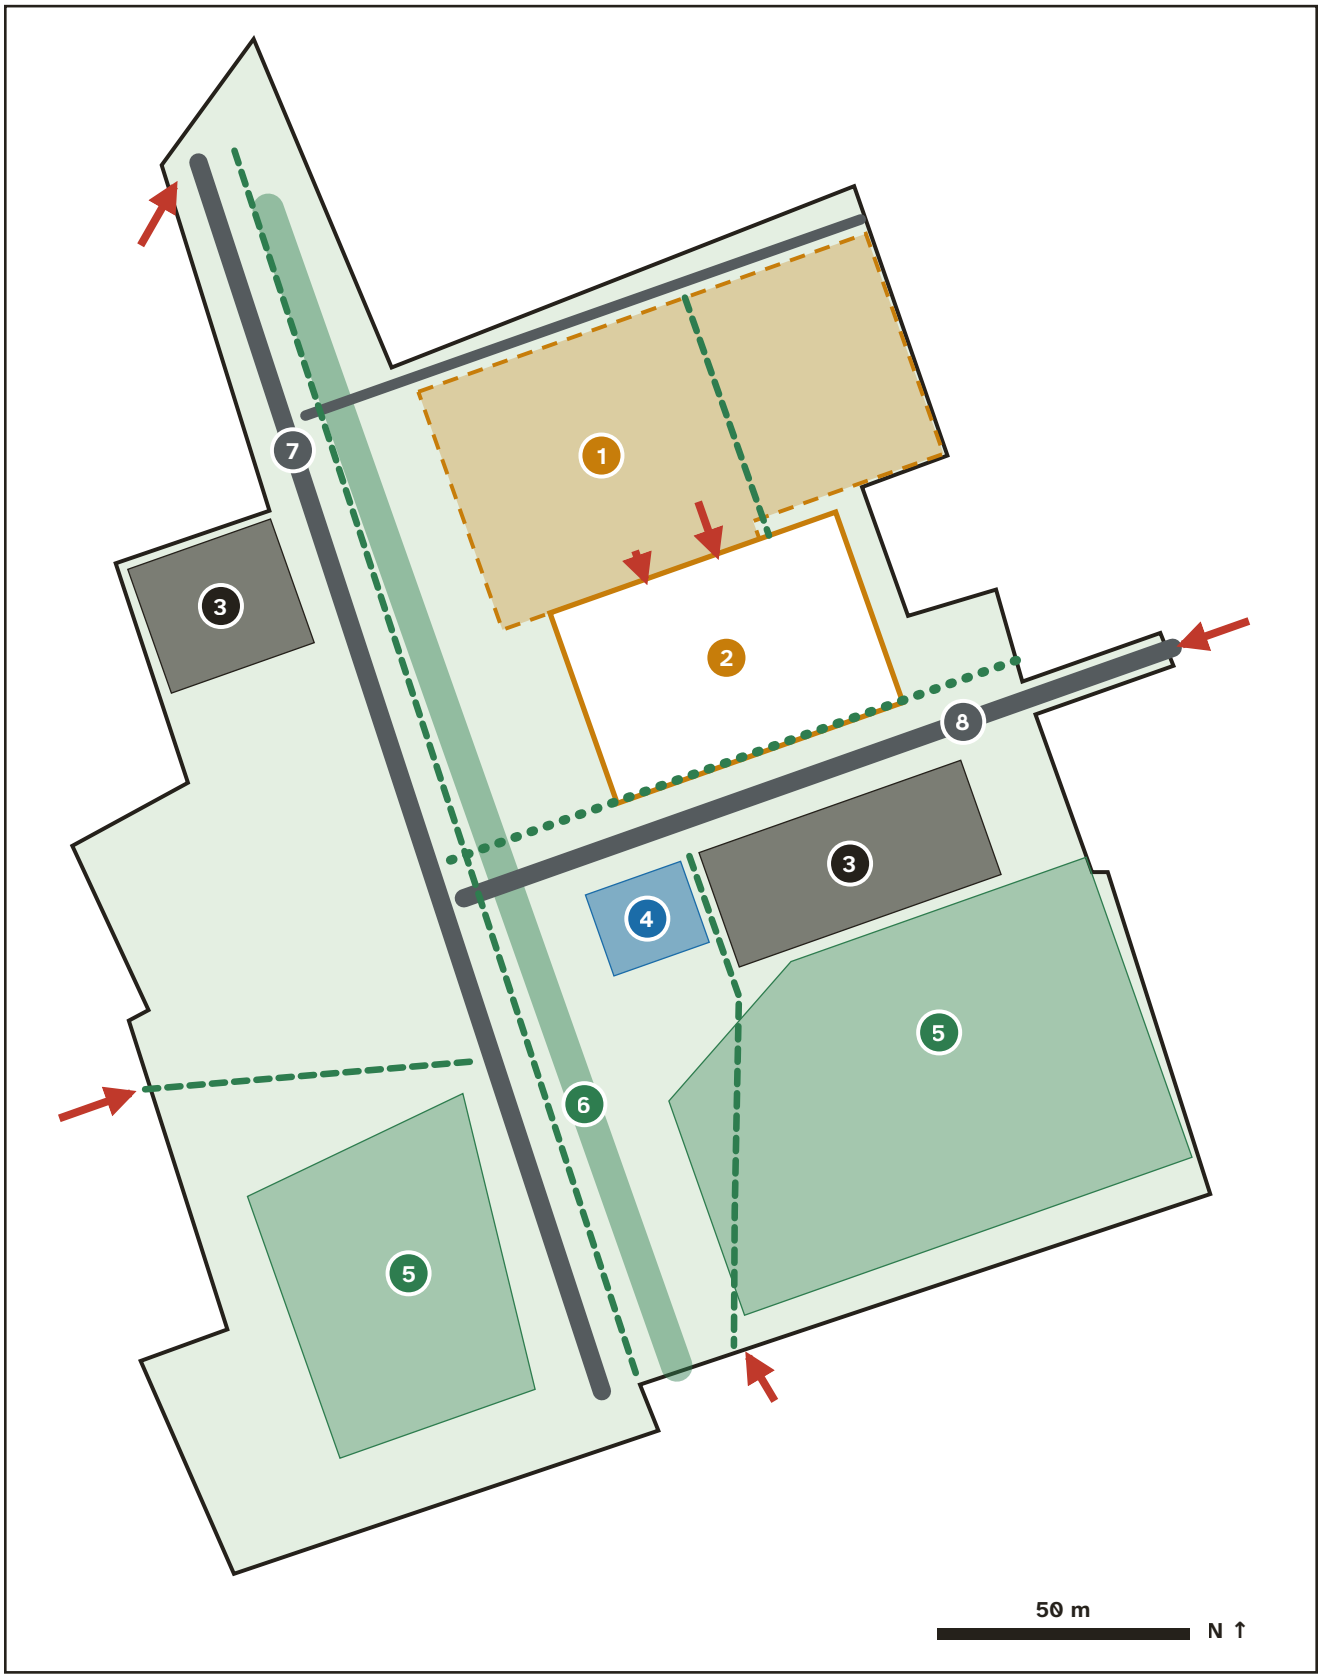

1 **Area edificabile, prescrittiva**
Concentra tutta la SF di 3.900 mq. Dentro l'area la forma dei lotti può cambiare.

2 **Piazza, prescrittiva**
Almeno 2.000 mq, pedonale, con fronte commerciale obbligatorio (frecce rosse).

3 **Parcheggi pubblici**
Almeno 2.043,5 mq. La posizione è indicativa, la quantità no.

4 **Attrezzature**
Almeno 331,5 mq, oppure diversa destinazione motivata dal piano.

5 **Boschi da conservare**
Nessuna edificazione. Sentieri permeabili ammessi.

6 **Fascia vegetata**
Si conserva. Attraversamenti solo nei due punti indicati.

7 **Strada esistente**
Ristrutturata: carreggiata, marciapiede, ciclabile separata.

8 **Nuovi tratti**
Collegamento con la via a est, prescrittivo. Filare obbligatorio a nord.

Frecce rosse sui bordi: varchi e connessioni con il contesto. Frecce rosse sull'area: fronte commerciale sulla piazza.

Voce della scheda	Contenuto
Strumento	Piano attuativo convenzionato (LR 65, art. 95 c. 3 lett. a; artt. 107, 109). Durata della previsione: quinquennale (art. 95 c. 1 lett. b)
Parametri	ST 40.150 · SF 3.900 · SE 6.300, con residenza 1.260, ERS 250, direzionale 4.290, commercio di vicinato 500
Altezze	Residenza 2 piani; direzionale fino a 3 piani
Indice di copertura massimo	Proposta: 65% della SF
Dotazioni minime	Parcheggi pubblici 2.043,5; standard totali 4.750; piazza almeno 2.000 mq
Opere a carico	Riordino della strada, nuovo collegamento, rete ciclopedonale, piazza, parco: cessione e realizzazione in convenzione
Prescrizioni	Conservare i boschi e la fascia vegetata; autorimesse interrate entro il limite di permeabilità; fronte commerciale sulla piazza; nessuna auto in piazza
Da verificare prima del piano	Territorio urbanizzato, rischio idraulico, fattibilità (art. 95 c. 5 lett. c), fascia ferroviaria, VAS o esclusione (LR 10, art. 5 bis c. 2)
Indicativo	Forma dei lotti, posizione dei parcheggi, tracciati nel parco

7. Relazione modello

Impostazione. L'area è libera e il programma contiene residenza: l'intervento presuppone che ricada nel territorio urbanizzato (LR 65, art. 4 c. 2), da riscontrare sul piano strutturale. Non presentando degrado né patrimonio dismesso, non è un intervento ai sensi dell'art. 125: è un piano attuativo previsto dal piano operativo (artt. 95, 107, 109), con scheda norma. Il fine pubblico è dare un centro e una rete a un insediamento che oggi non li ha (art. 62 c. 1 lett. b, d).

Impianto. La strada esistente diventa un viale con ciclabile. Un nuovo tratto la collega alla via a est, attraverso il varco già compreso nel perimetro. All'incrocio sorge il centro: una piazza di 2.400 mq, chiusa a nord da un edificio di 3 piani con negozi e uffici, affiancata da residenza ed ERS su 2 piani.

Spazi aperti. La SF è il 9,7% della ST. Il resto è pubblico: 25.179 mq di verde, in gran parte boschi esistenti, conservati e resi percorribili. La gestione è il vero costo: va regolata in convenzione.

Verifiche. Standard minimi 4.750 mq (DM 1444, artt. 3 e 5), parcheggi pubblici 2.100 su 2.043,5 minimi. Pertinenziali 1.915 mq (art. 41-sexies L. 1150/42; DPGR 39/R, artt. 24 e 37) e relazione 300 mq sulla vendita ipotizzata (DPGR 23/R, artt. 8 e 9). La SF non basta per la sosta a raso (1.548 mq liberi): prevedo autorimesse interrate, contenute per salvare il 25% permeabile (DPGR 39/R, artt. 25 e 26).

> **Limiti.** La foto non dice quote, specie, natura della fascia vegetata, rischio idraulico. Il disegno va verificato con le indagini di fattibilità e con la fascia ferroviaria.

8. Come disegnarlo a mano

- **Ordine:** perimetro, strade, piazza, lotti, edifici, parcheggi, boschi, filari. Le scritte per ultime.
- **A 1:1000:** 1 mm vale 1 m. La piazza è 60 × 40 mm, un posto auto 2,5 × 5 mm.
- **Griglia:** traccia a matita una griglia di 10 mm parallela alla strada: è il sistema di questa tavola.
- **Interrati:** tratteggiali, con i mq scritti accanto.
- **Boschi:** macchie a pennarello, non cerchietti uno a uno: risparmi molto tempo.
- **Scheda norma:** rifalla piccola, solo con cinque o sei segni. Distingui con la legenda ciò che è obbligo.

9. Cosa portare a memoria

- **Le quattro superfici:** standard pubblici, pertinenziali, relazione, permeabile. Si sommano, non si scambiano.
- **Permeabile e interrati:** un solaio sotto terra non è permeabile (DPGR 39/R, art. 25 c. 1).
- **Copertura:** SE ÷ piani, somma, dividi per SF. Fallo sempre quando la traccia dà la SF.
- **Art. 4 c. 2:** niente nuova residenza fuori dal territorio urbanizzato.
- **Rigenerazione:** art. 125 solo con degrado (artt. 122, 123). Un'area libera è un'altra cosa.
- **ERS:** art. 63, standard aggiuntivo.

10. Su quali altre tracce riusarlo

Traccia	Cosa tieni	Cosa cambi
2024 T2	Conti, bilancio, sezioni	Niente SF data; c'è il produttivo e l'asse è imposto
2018 II T1	Conti e scheda	Aggiungi la bozza di convenzione
2014 I T2 e 2016 II T2	Conti e planivolumetrico	Indice in mc/mq; proposta di nuovi standard
2026 I T2	Parco e margine, scheda	Il parco agrourbano diventa centrale

11. Cosa ho verificato e cosa no

- **Riscontrato sui testi:** DM 1444/68, artt. 3, 5 e 9; DPGR 39/R/2018, artt. 2, 10, 16, 24-26, 37 e 39; DPGR 23/R/2020, artt. 8 e 9; LR 65, artt. 4, 62, 63, 95, 107, 109, 122, 123 e 125; LR 10, art. 5 bis; L. 1150/42, art. 41-sexies su Normattiva.
- **Misurato:** perimetro ricalcato sulla linea rossa dell'allegato A. La scala nasce dalla ST: circa 0,26 m per pixel a 200 dpi, cioè circa 1:2.049 sulla pagina. La strada risulta larga circa 9 m, un valore plausibile: ma i mq sono indicativi.
- **Mancante:** l'allegato B non è nel PDF. Non ho quote, strumenti urbanistici, vincoli, rischio idraulico, né il nome del luogo.
- **Da riscontrare:** se la fascia vegetata è un corso d'acqua del reticolo (allora 10 m, LR 41/2018, art. 3); fascia di rispetto ferroviaria (norma non controllata); categoria delle strade (DM 5/11/2001, non controllato); applicabilità della zona C.

- **Mie ipotesi:** nord in alto, 300 mq di vendita, commercio al piano terra del direzionale, 85 mq per alloggio, piazza contata nella quota dell'art. 5 n. 2, indice di copertura, sezioni. Sono una soluzione tra le possibili, non quella attesa dalla commissione.